



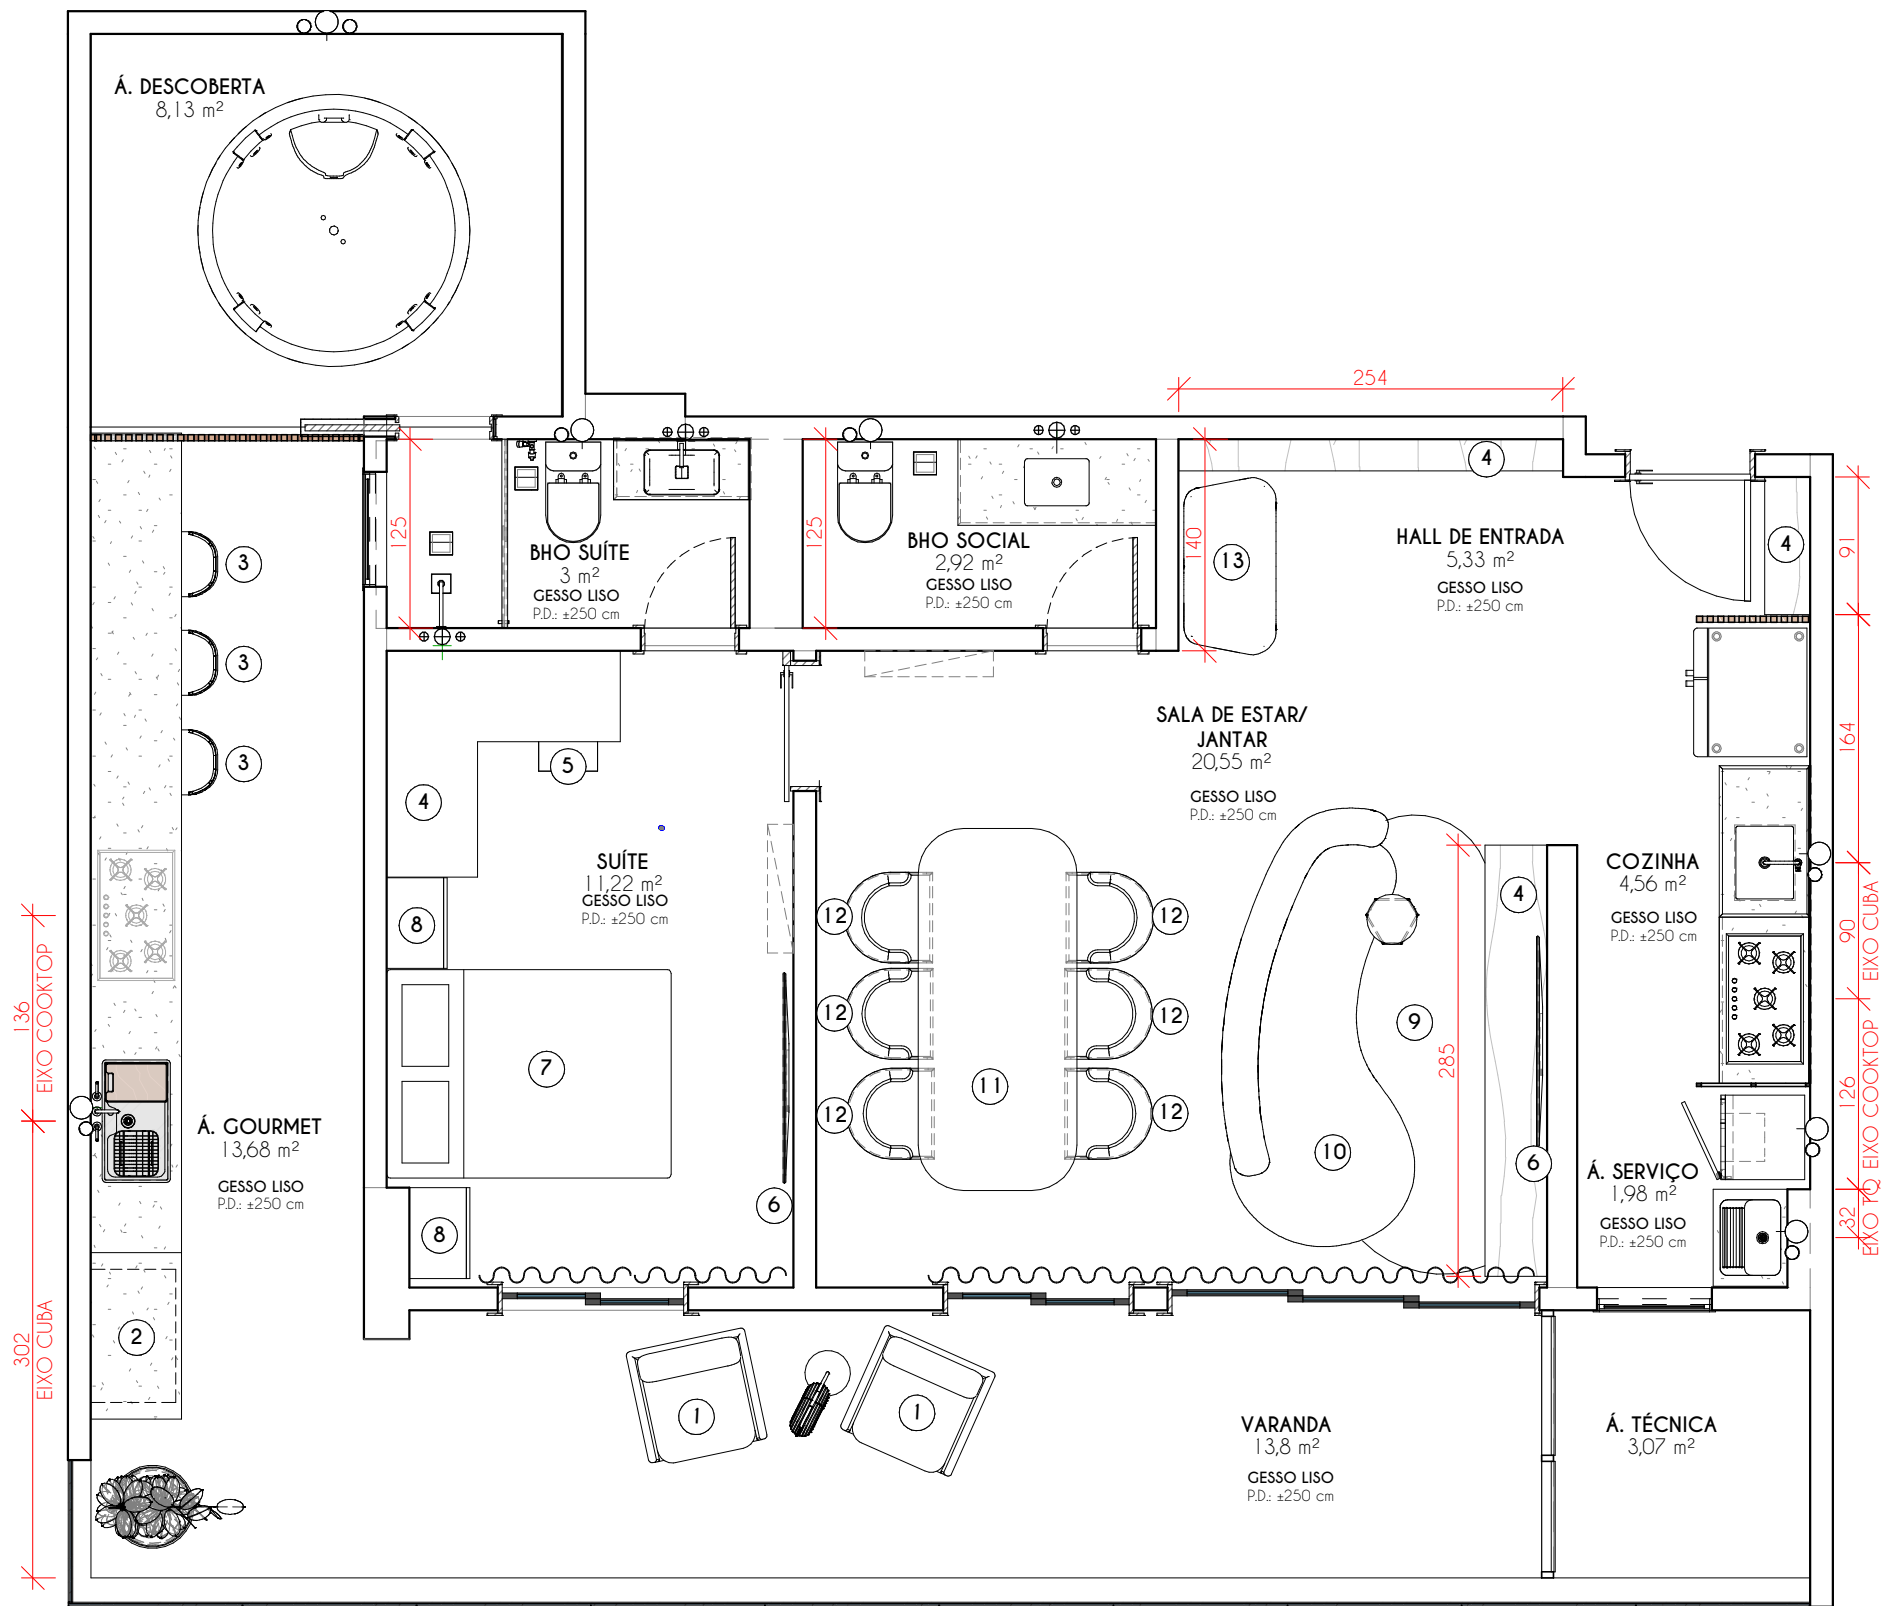

PLANTA BAIXA - AMBIENTAÇÃO

ESCALA 1 : 50


LEGENDA - MOBILIÁRIO	
VARANDA:	
1	POLTRONA LENA- FREIJÓ E LINHO BEGE- MÓVEIS GRUBER SKU 9.178.265.T02
ÁREA GOURMET:	
2	CHURRASQUEIRA INOX- EMPÓRIO NOBRE CG16
3	BANQUETA LORIENTE AREIA/ AMÊNDOA- ATTRAKTIVA BQ2518
QUARTO:	
4	MOBILIÁRIO EM MARCENARIA MDF CONNECT- ARAUCO
5	PUFF REDONDO- DAKOTA 525441
6	TELEVISÃO VISION AI- SAMSUNG QN50Q7FAACXZD
7	CAMA CASAL QUEEN SUSPensa 1572269538- LEROY MERLIN
8	MESA DE CABECEIRA BRIANNA- MÓVEIS GRUBER SKU 27933 HNV.PR
SALA:	
9	TAPETE SEED BOUCLÉ CAPRI NATURAL- SÃO JOSÉ TAPETES
10	SOFÁ ORGÂNICO COM CHAISE MODULAR IA BEAN- SOFT
11	MESA ORGÂNICA ISLA JEQUITIBÁ NATURAL- LILIBEE 135903449
12	CADEIRA MATERA- ATTRAKTIVA PO13921
13	PUFF LIVING AISHA ORGÂNICO- DECK DESING
OBS: COZINHA E BANHEIRO- VER DETALHAMENTO	

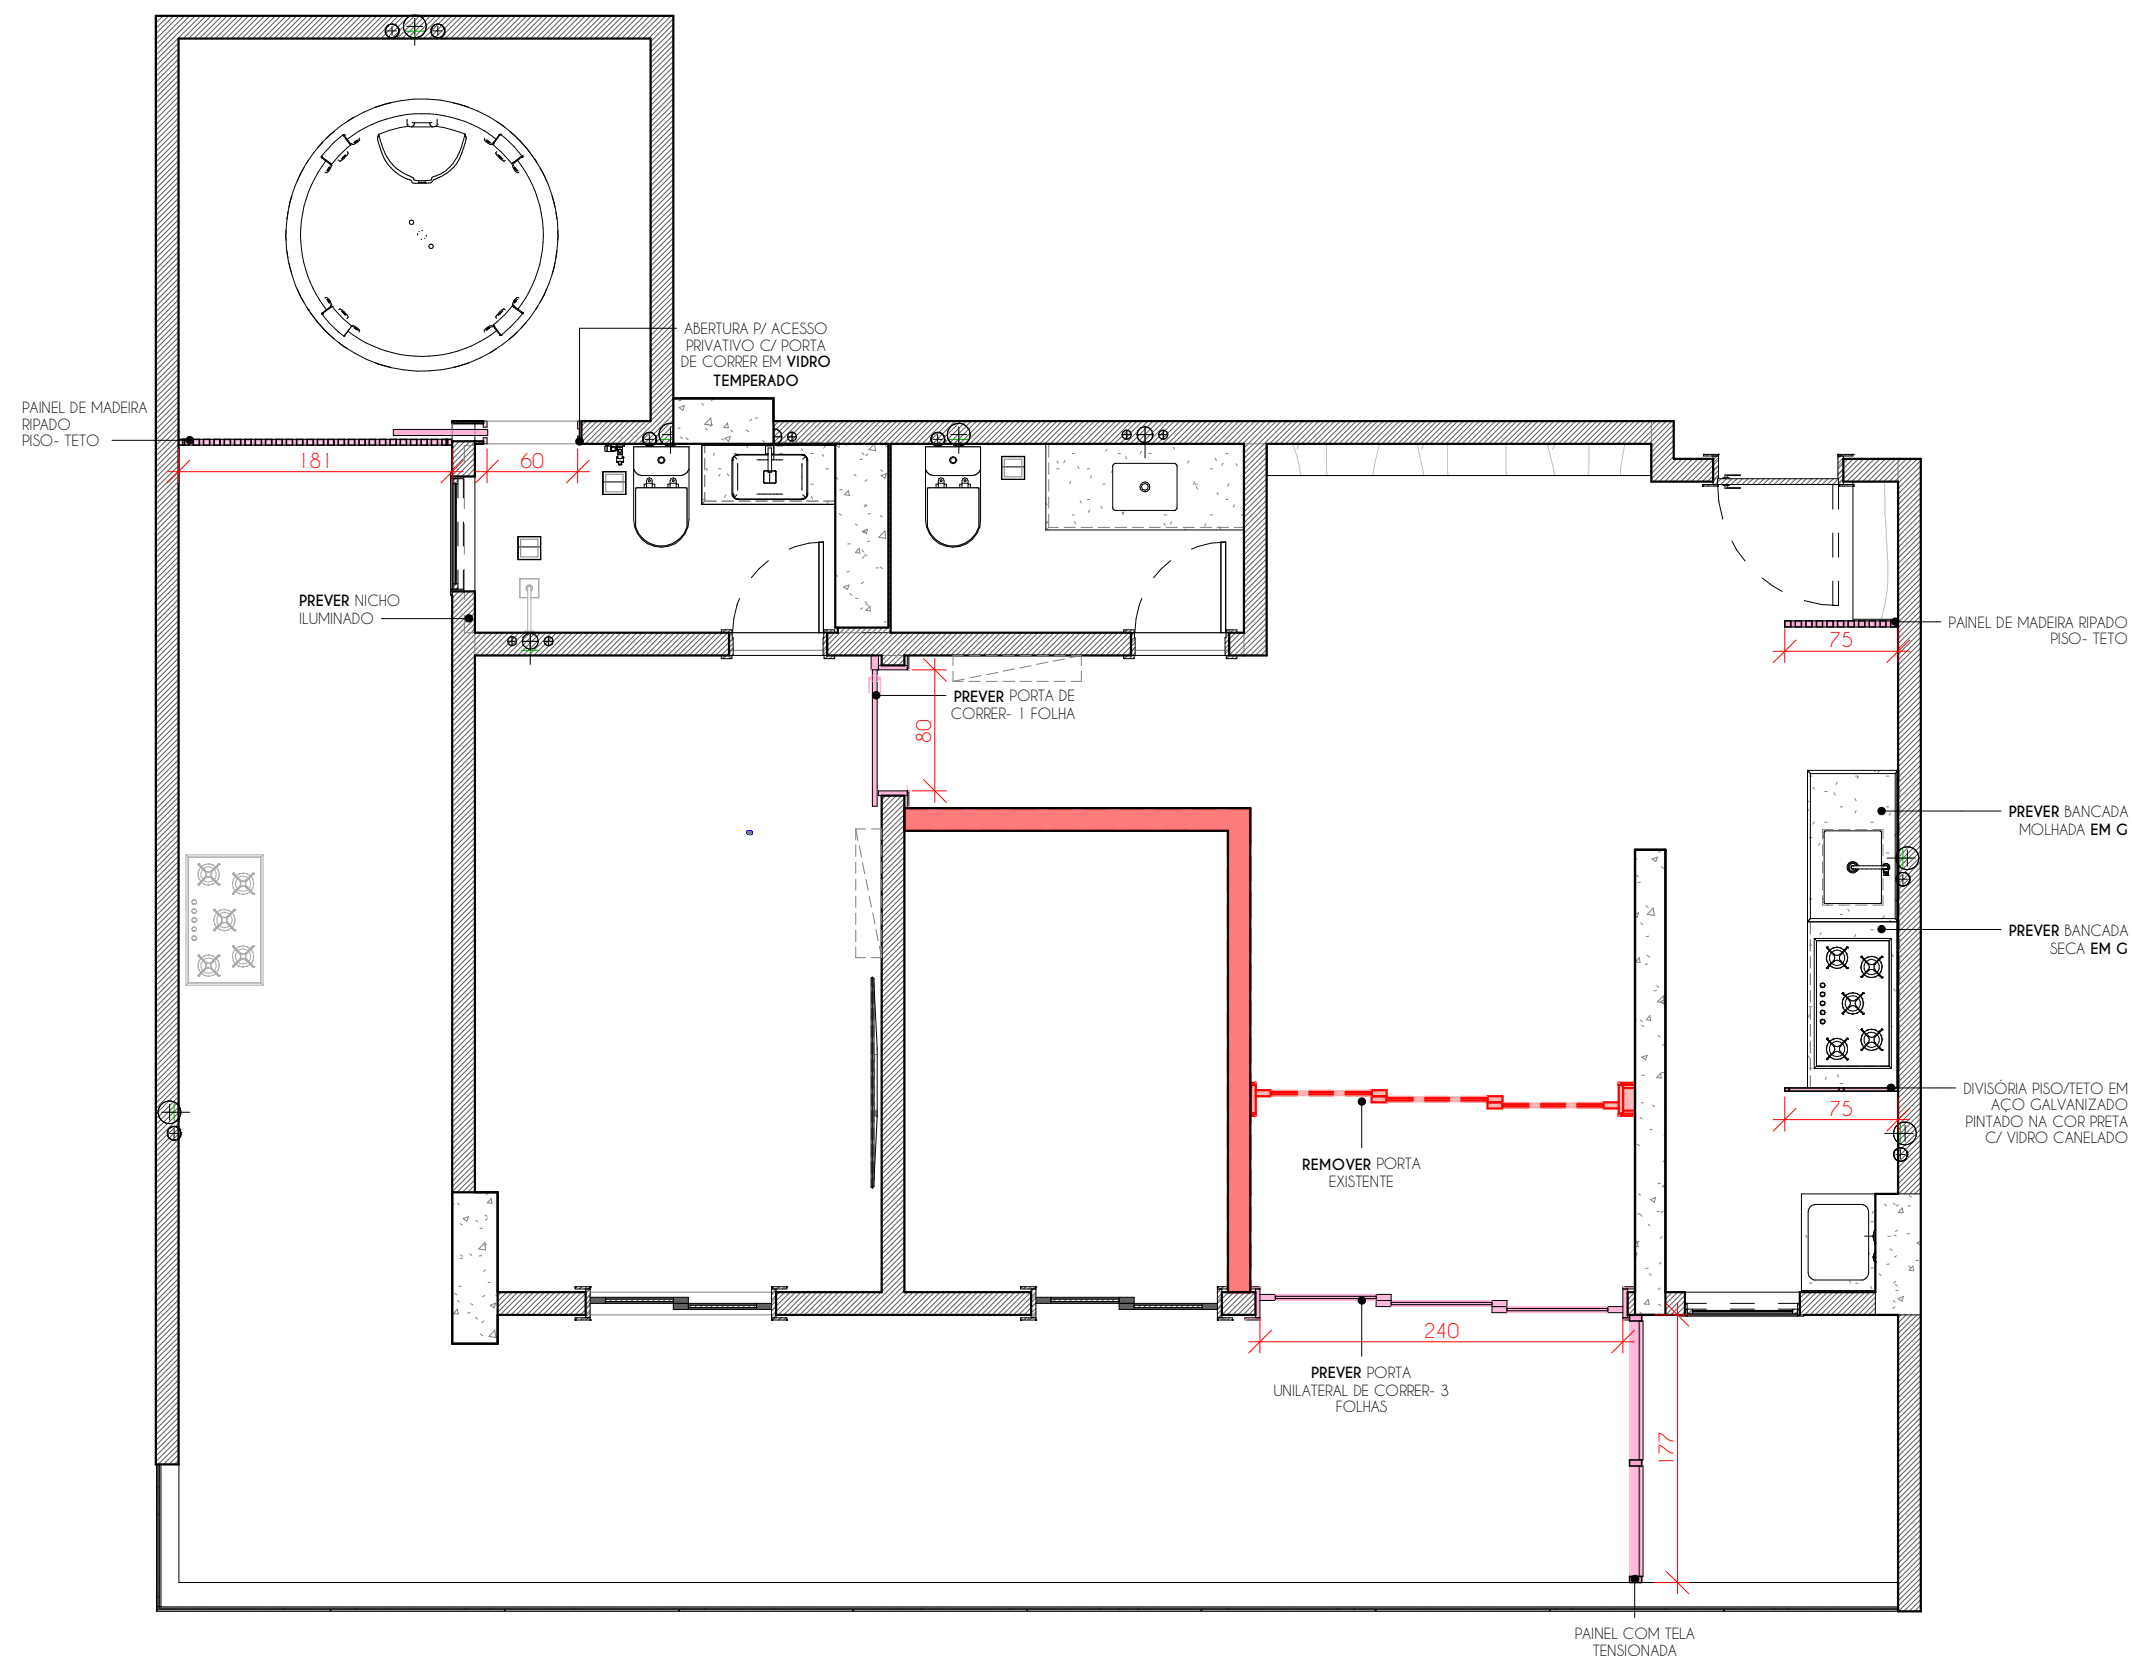

PLANTA BAIXA- DEMOLIÇÃO E CONSTRUÇÃO
ESCALA 1 : 50

LEGENDA - MODIFICAÇÃO DE PAREDES	
	ALVENARIA EXISTENTE
	A CONSTRUIR
	A DEMOLIR
	PILAR EXISTENTE


	MATÉRIA: ARQUITETURA E PLANEJAMENTO DE INTERIORES	TÍTULO: DEMOLIÇÃO E CONSTRUÇÃO	DATA: JUNHO/2025	PRANCHA: 02.07
	INTEGRANTES: Mariana Gottardo, Emanuelly Ferreira e Karolaine Kohler	OBRA: Apartamento Airbnb	ORIENTADO POR: Priscilla Silva Loureiro e Erica Coelho Pagel	

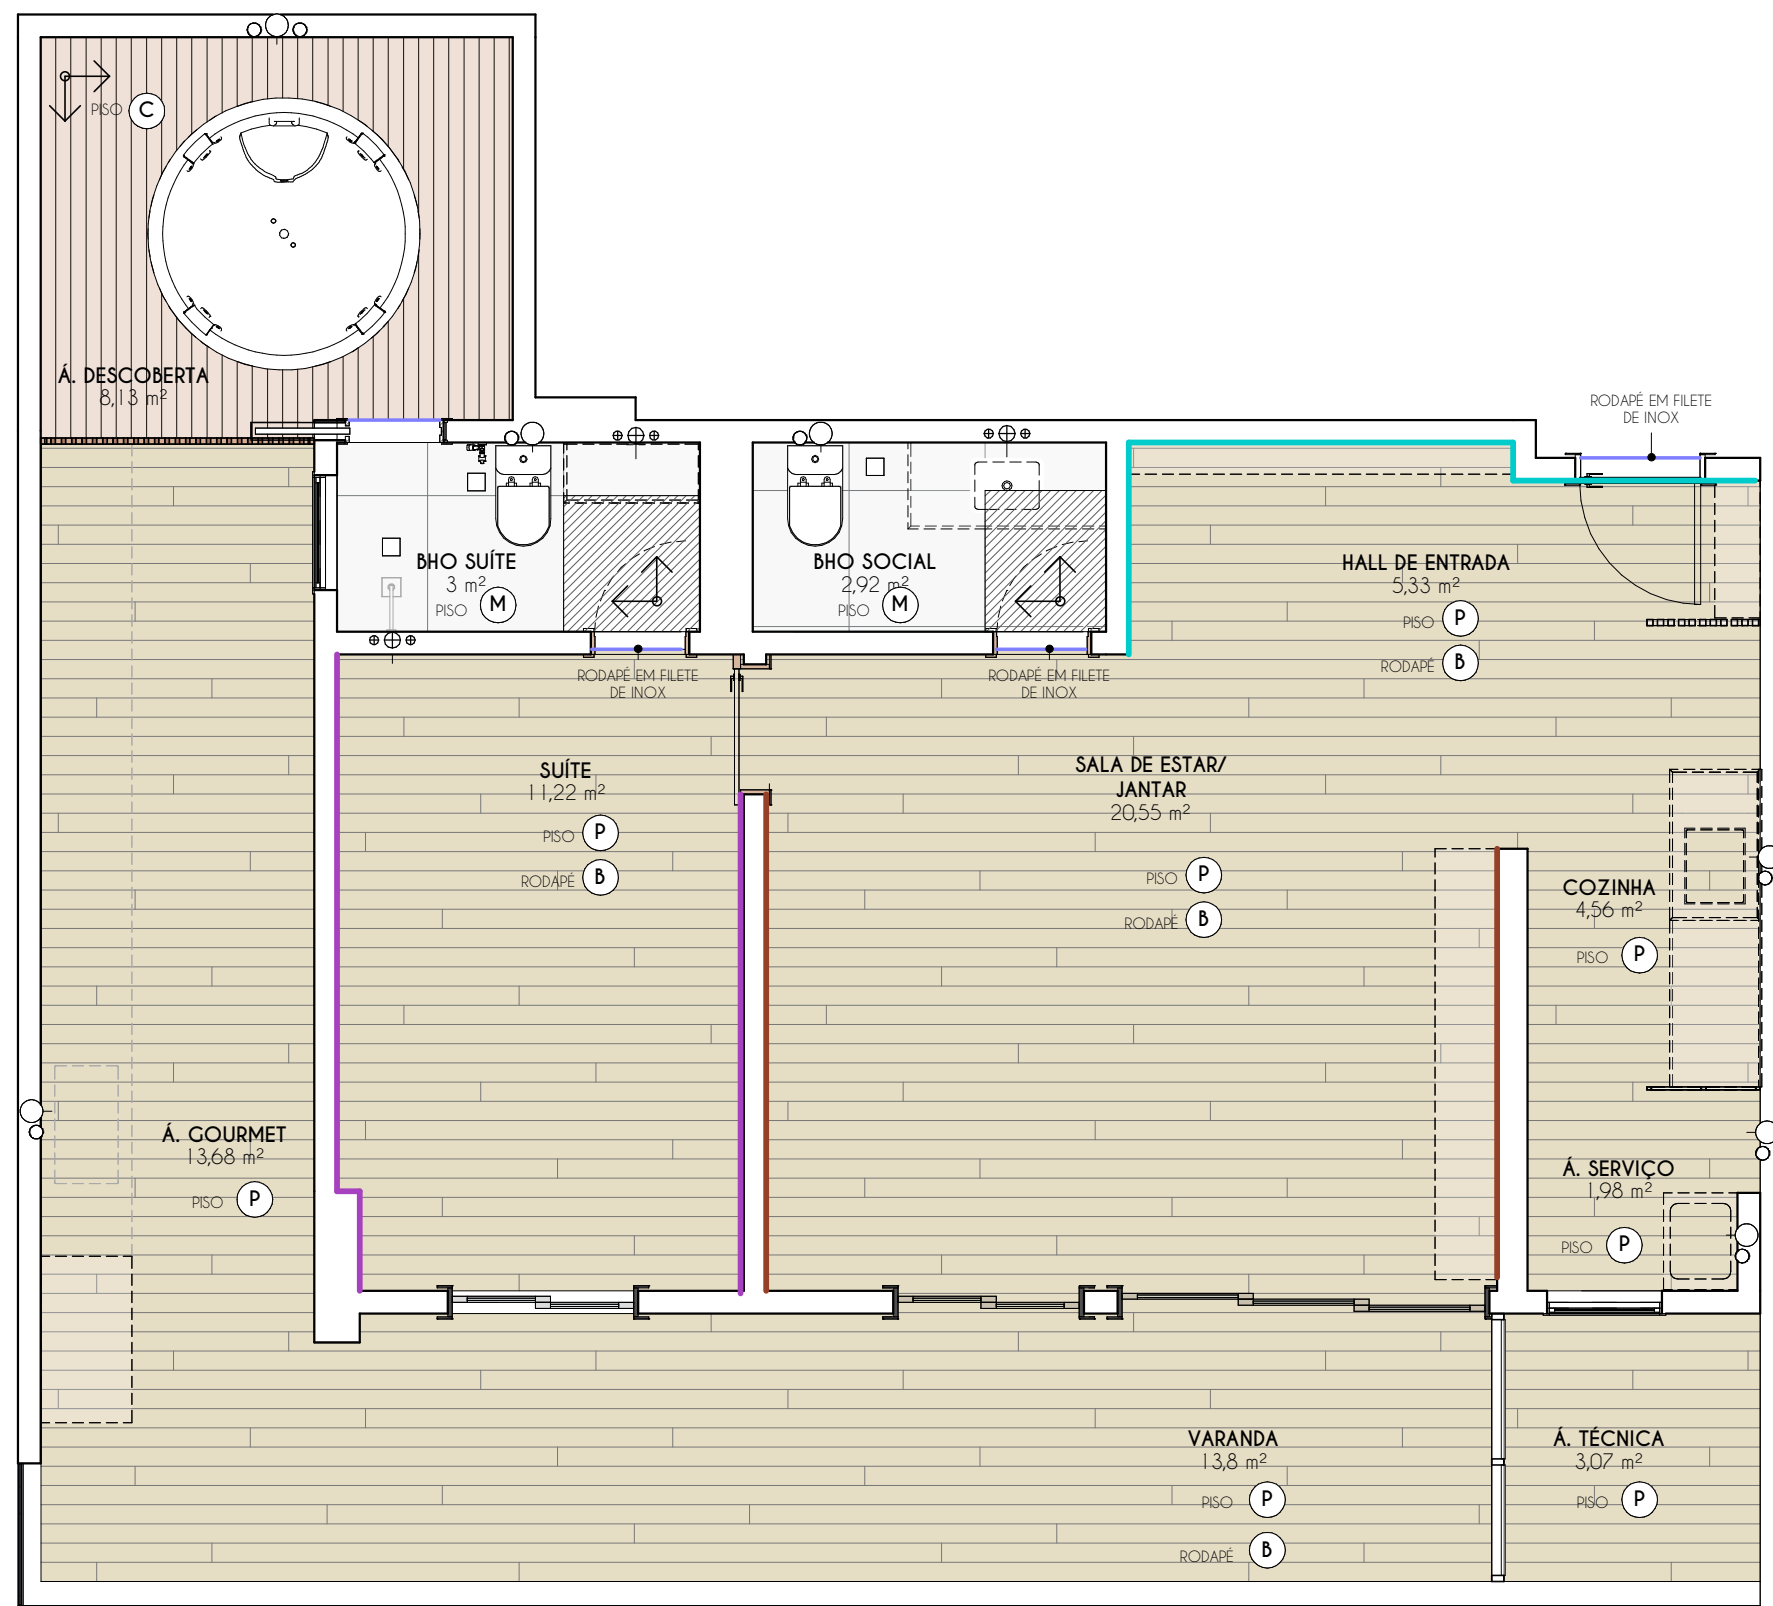

PLANTA BAIXA- PAG. PISO E ACABAMENTOS
ESCALA 1 : 50


LEGENDA - ACABAMENTOS	
	TINTA COR BARBOSA- SUVINIL
	TEXTURA POEIRA BRILHANTE- DIORE
	PARADE REVESTIDA EM MDF JEQUITIBÁ- ARAUCO
OBS: PREVER PINTURA DE TODO O APARTAMENTO EM TINTA LAVÁVEL BRANCA	

LEGENDA - ESPECIFICAÇÕES	
(M)	PORCELANATO CIMENTÍCIO MUNARI BRANCO 90x90- ELIANE
(P)	PISO VINÍLICO INJOY- PRÍMULA 208x1230mm- TARKETT
(C)	DECK MADEIRA CUMARU ROSA EXTRA- 10x300cm
(B)	RODAPÉ EM POLIESTIRENO NA COR BRANCA
OBS: CONFERIR MEDIDAS NO LOCAL; TODAS AS QUINAS TERÃO BIZOTE MÍNIMO;	

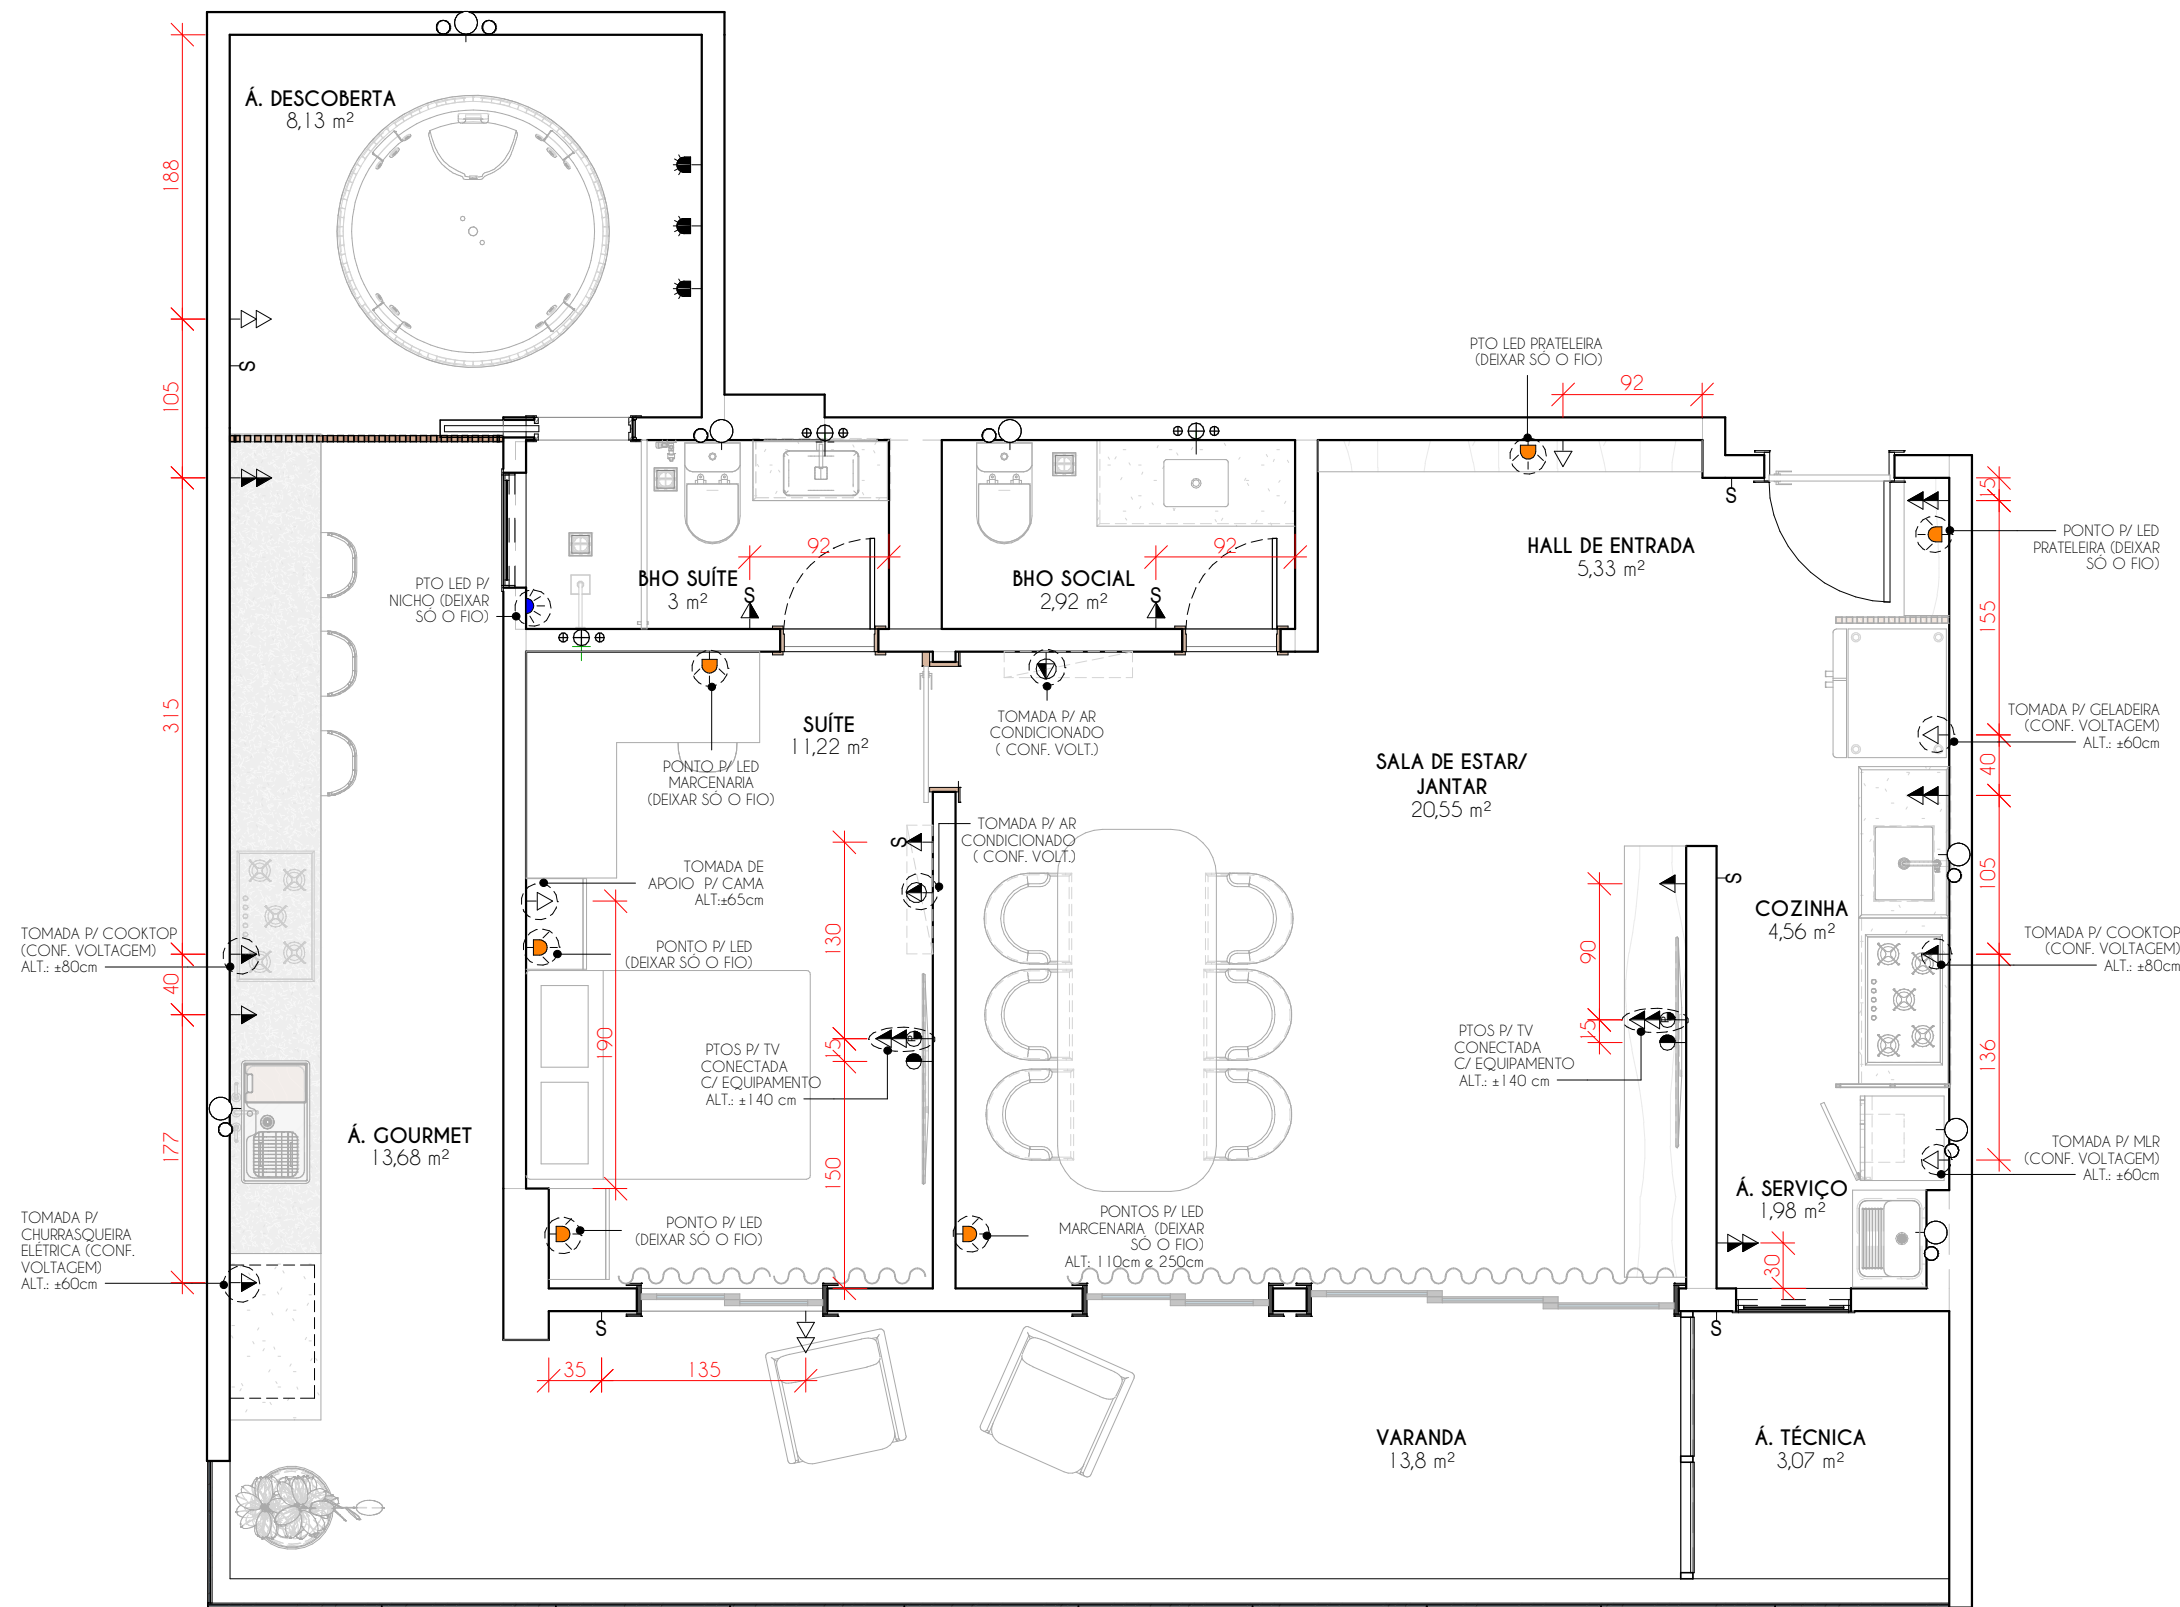


PLANTA BAIXA- PONTOS ELÉTRICOS
ESCALA 1 : 50


LEGENDA - ELÉTRICA		
		TOMADA BAIXA
		TOMADA BAIXA DUPLA
		TOMADA MÉDIA
		TOMADA MÉDIA DUPLA
		ANTENA
		TOMADA ALTA 20A
		PTO. LED (DEIXAR SÓ O FIO)
		PTO. LED NICHÔ (DEIXAR SÓ O FIO)
OBS: - VERIFICAR VOLTAGEM E AMPERES DOS EQUIPAMENTOS; - VERIFICAR ALTURAS DOS PONTOS EM PLANTA.		

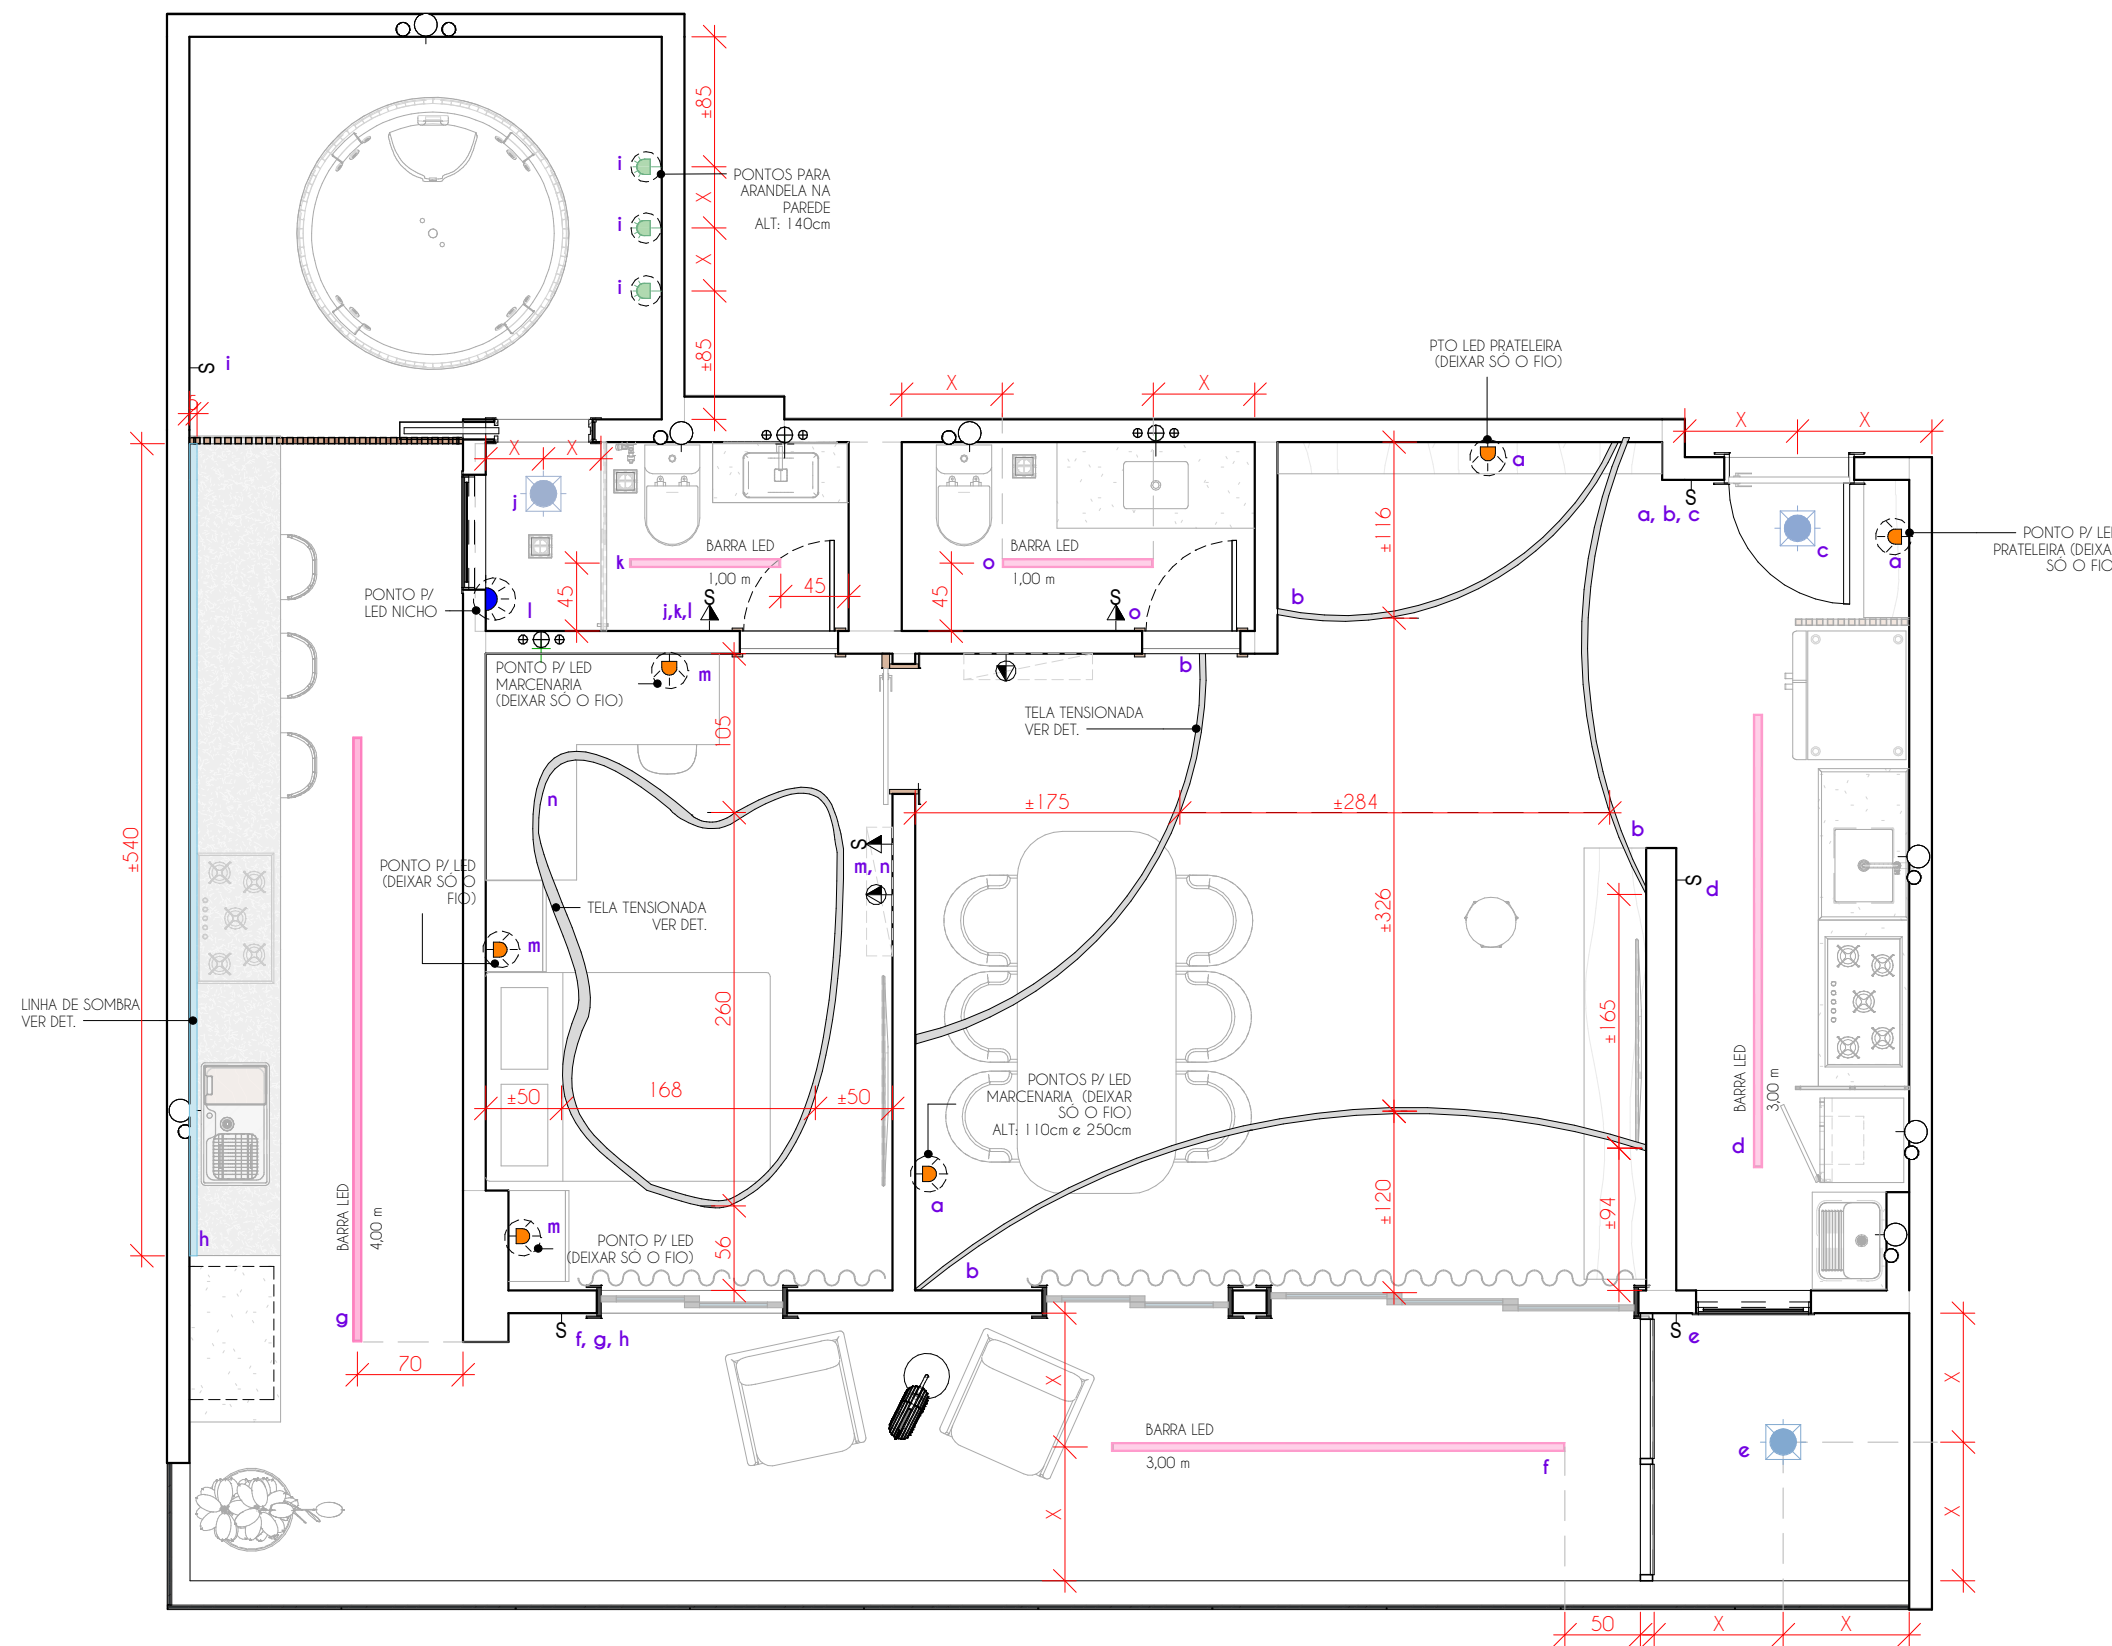

PLANTA BAIXA- ILUMINAÇÃO
ESCALA 1 : 50

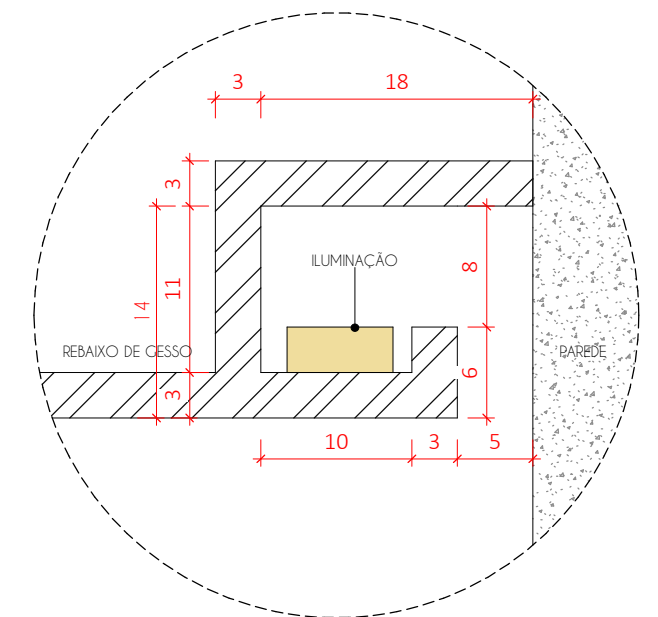


DET. LINHA DE SOMBRA
ESCALA 1 : 5

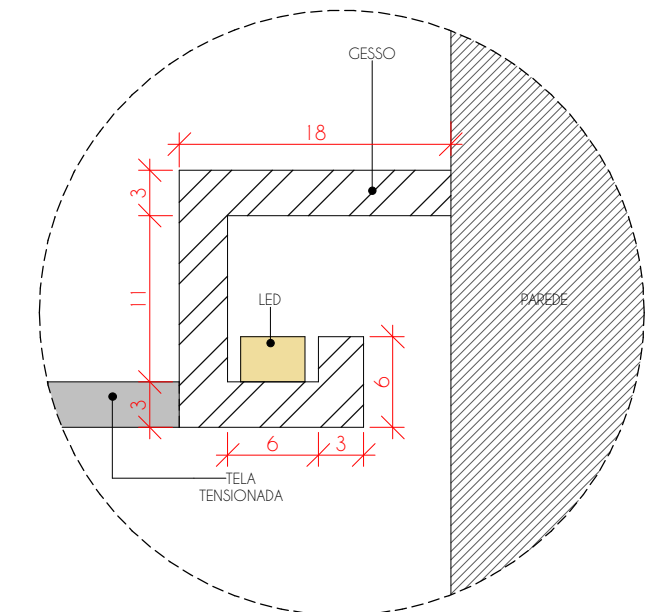


DET. TELA TENSIONADA
ESCALA 1 : 5


LEGENDA - LUMINÁRIAS		
	PAR 20	03
	PTO P/ ARANDELA (DEIXAR SÓ O FIO)	03
	LINHA DE SOMBRA ILUMINADA- VER DET.	01
	FITA LED PRA TELA TENSIONADA (VER TAMANHO NA PLANTA)	05
	BARRA LED- FITA 2 LADOS (VER TAMANHO NA PLANTA)	05
	PTO P/ FITA DE LED- NICHÔ BOX (DEIXAR SÓ O FIO)	01
	PTO DE LUZ P/ FITA DE LED (DEIXAR SÓ O FIO)	06

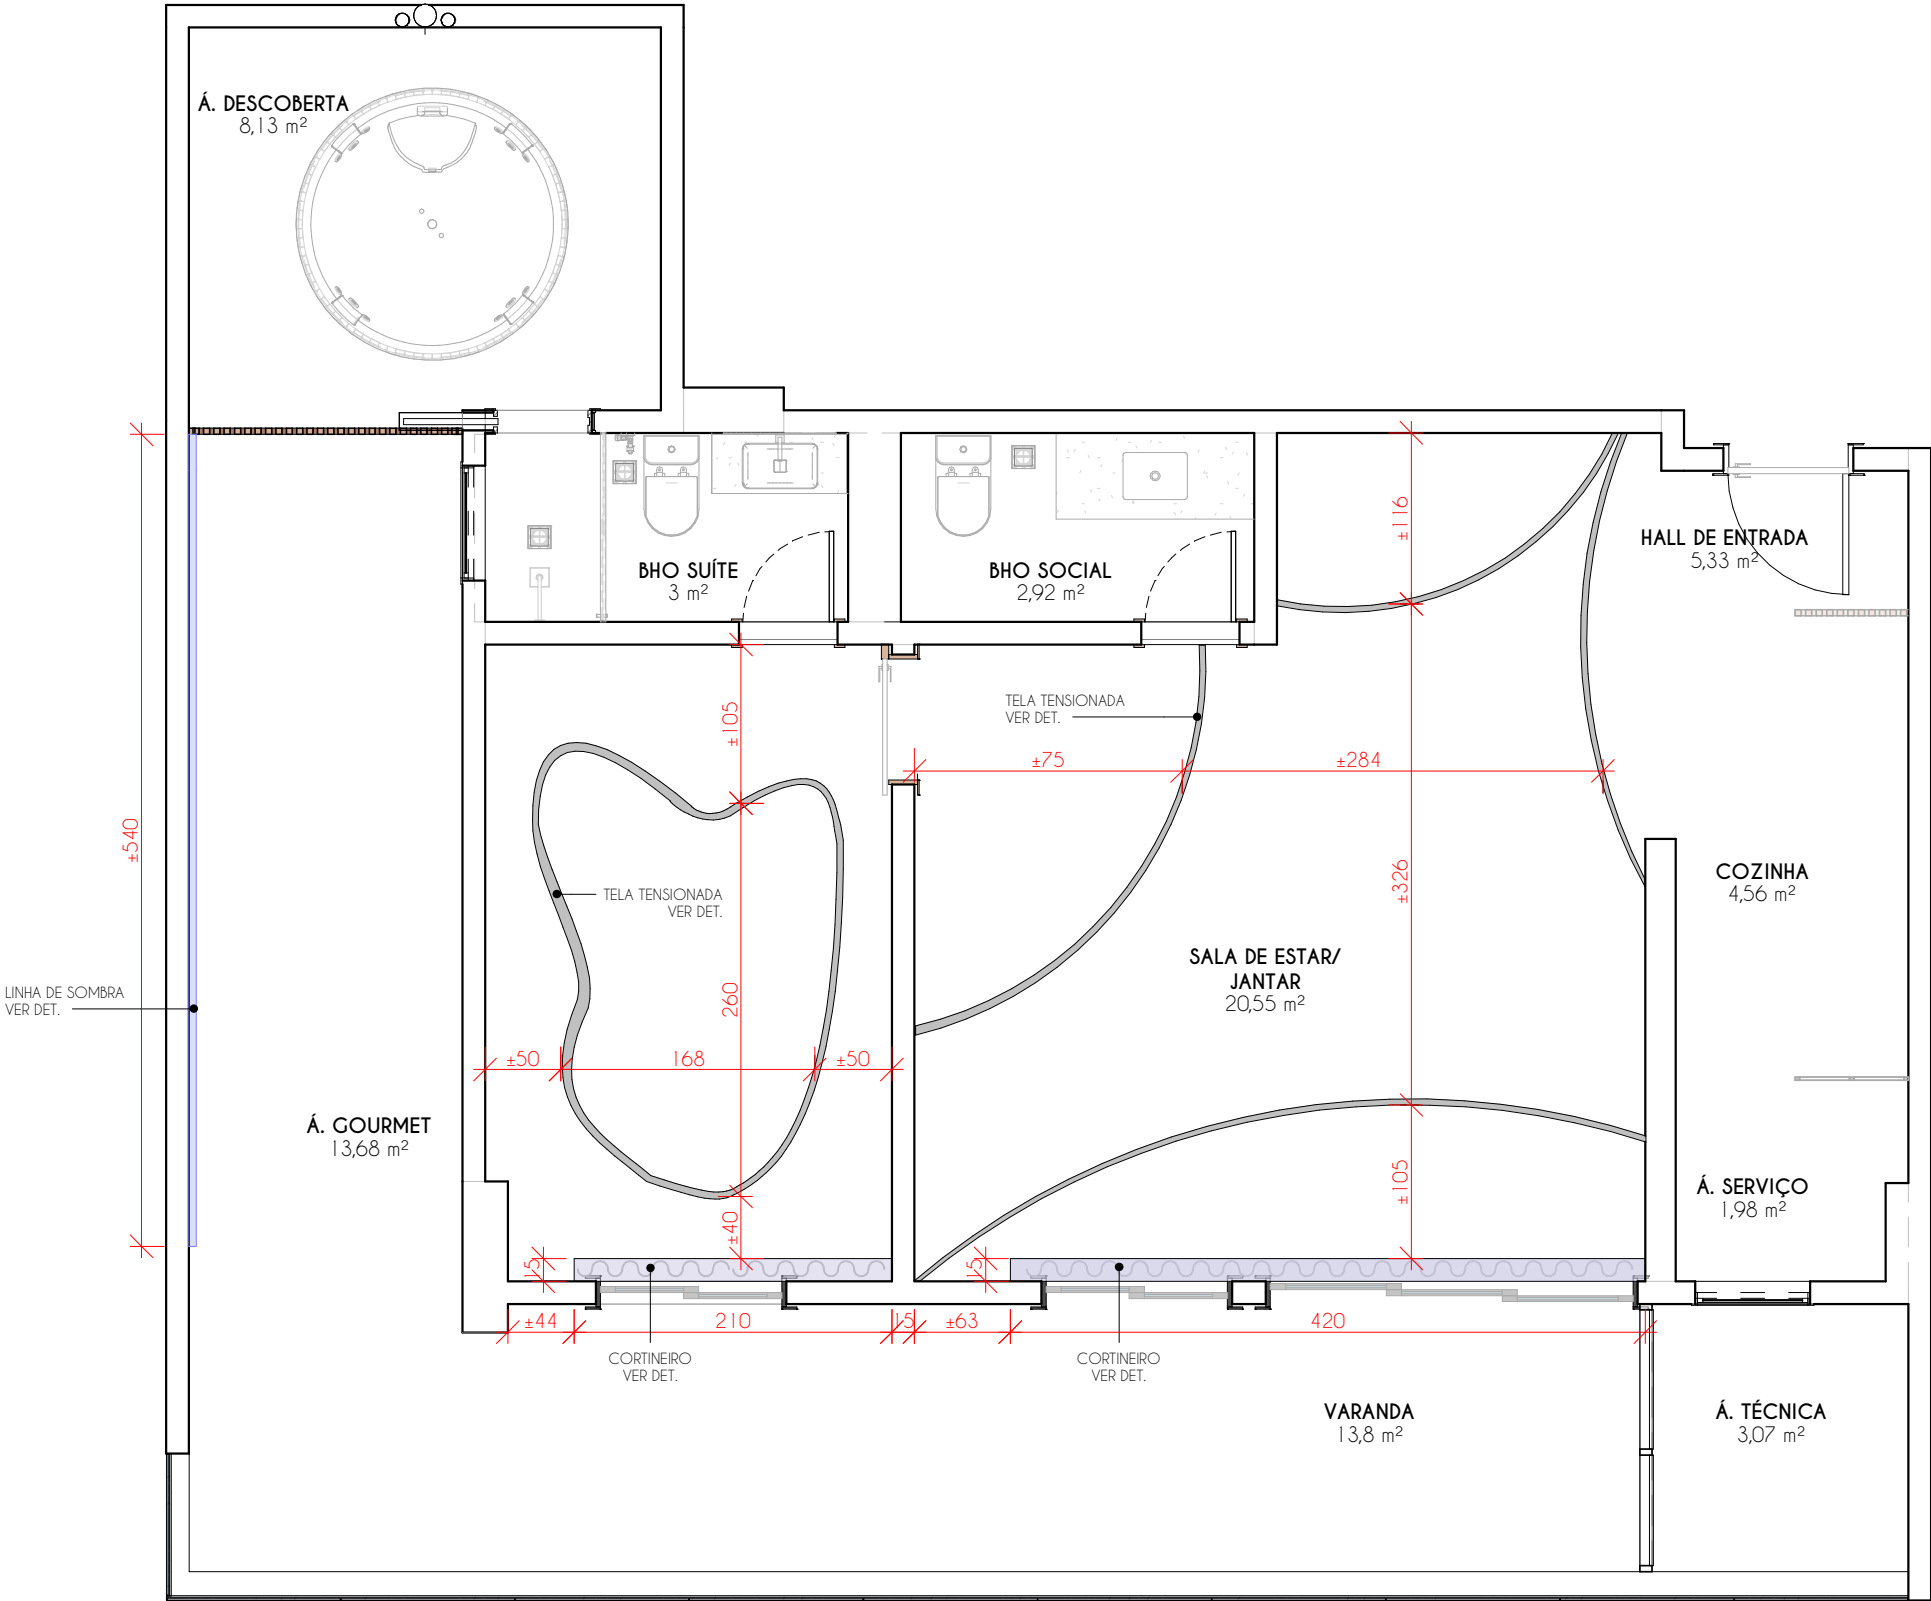


PLANTA BAIXA- GESSO
ESCALA 1 : 50

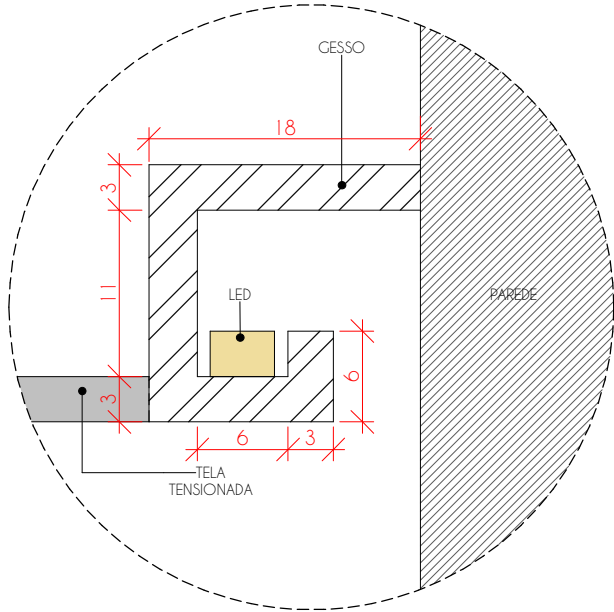

DET. TELA TENSIONADA
ESCALA 1 : 5

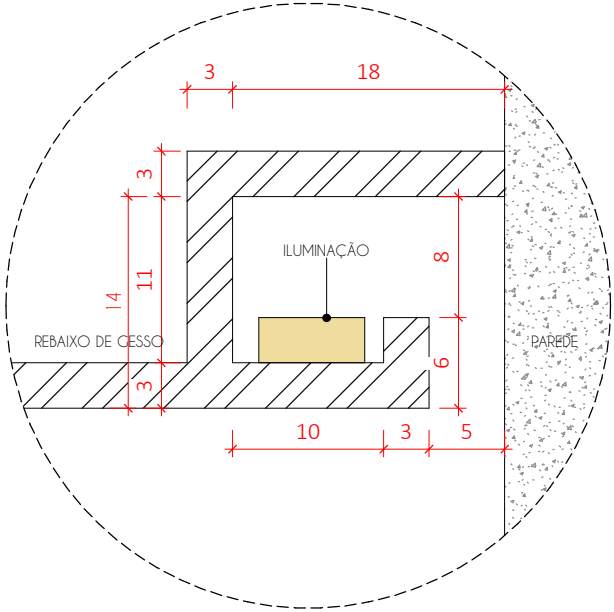


DET. LINHA DE SOMBRA
ESCALA 1 : 5

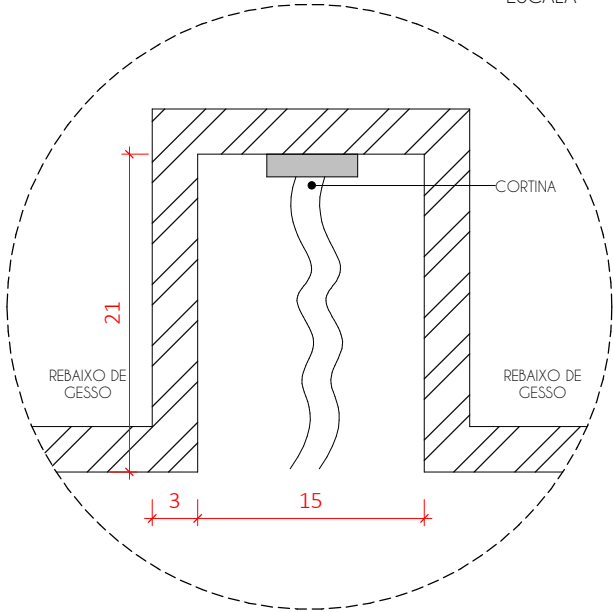

DET. CORTINEIRO
ESCALA 1 : 5

LEGENDA - GESSO

- CORTINEIRO (VER TAMANHO NA PLANTA)
- TELA TENSIONADA (VER TAMANHO NA PLANTA)
- LINHA DE SOMBRA ILUMINADA (VER DETALHAMENTO)

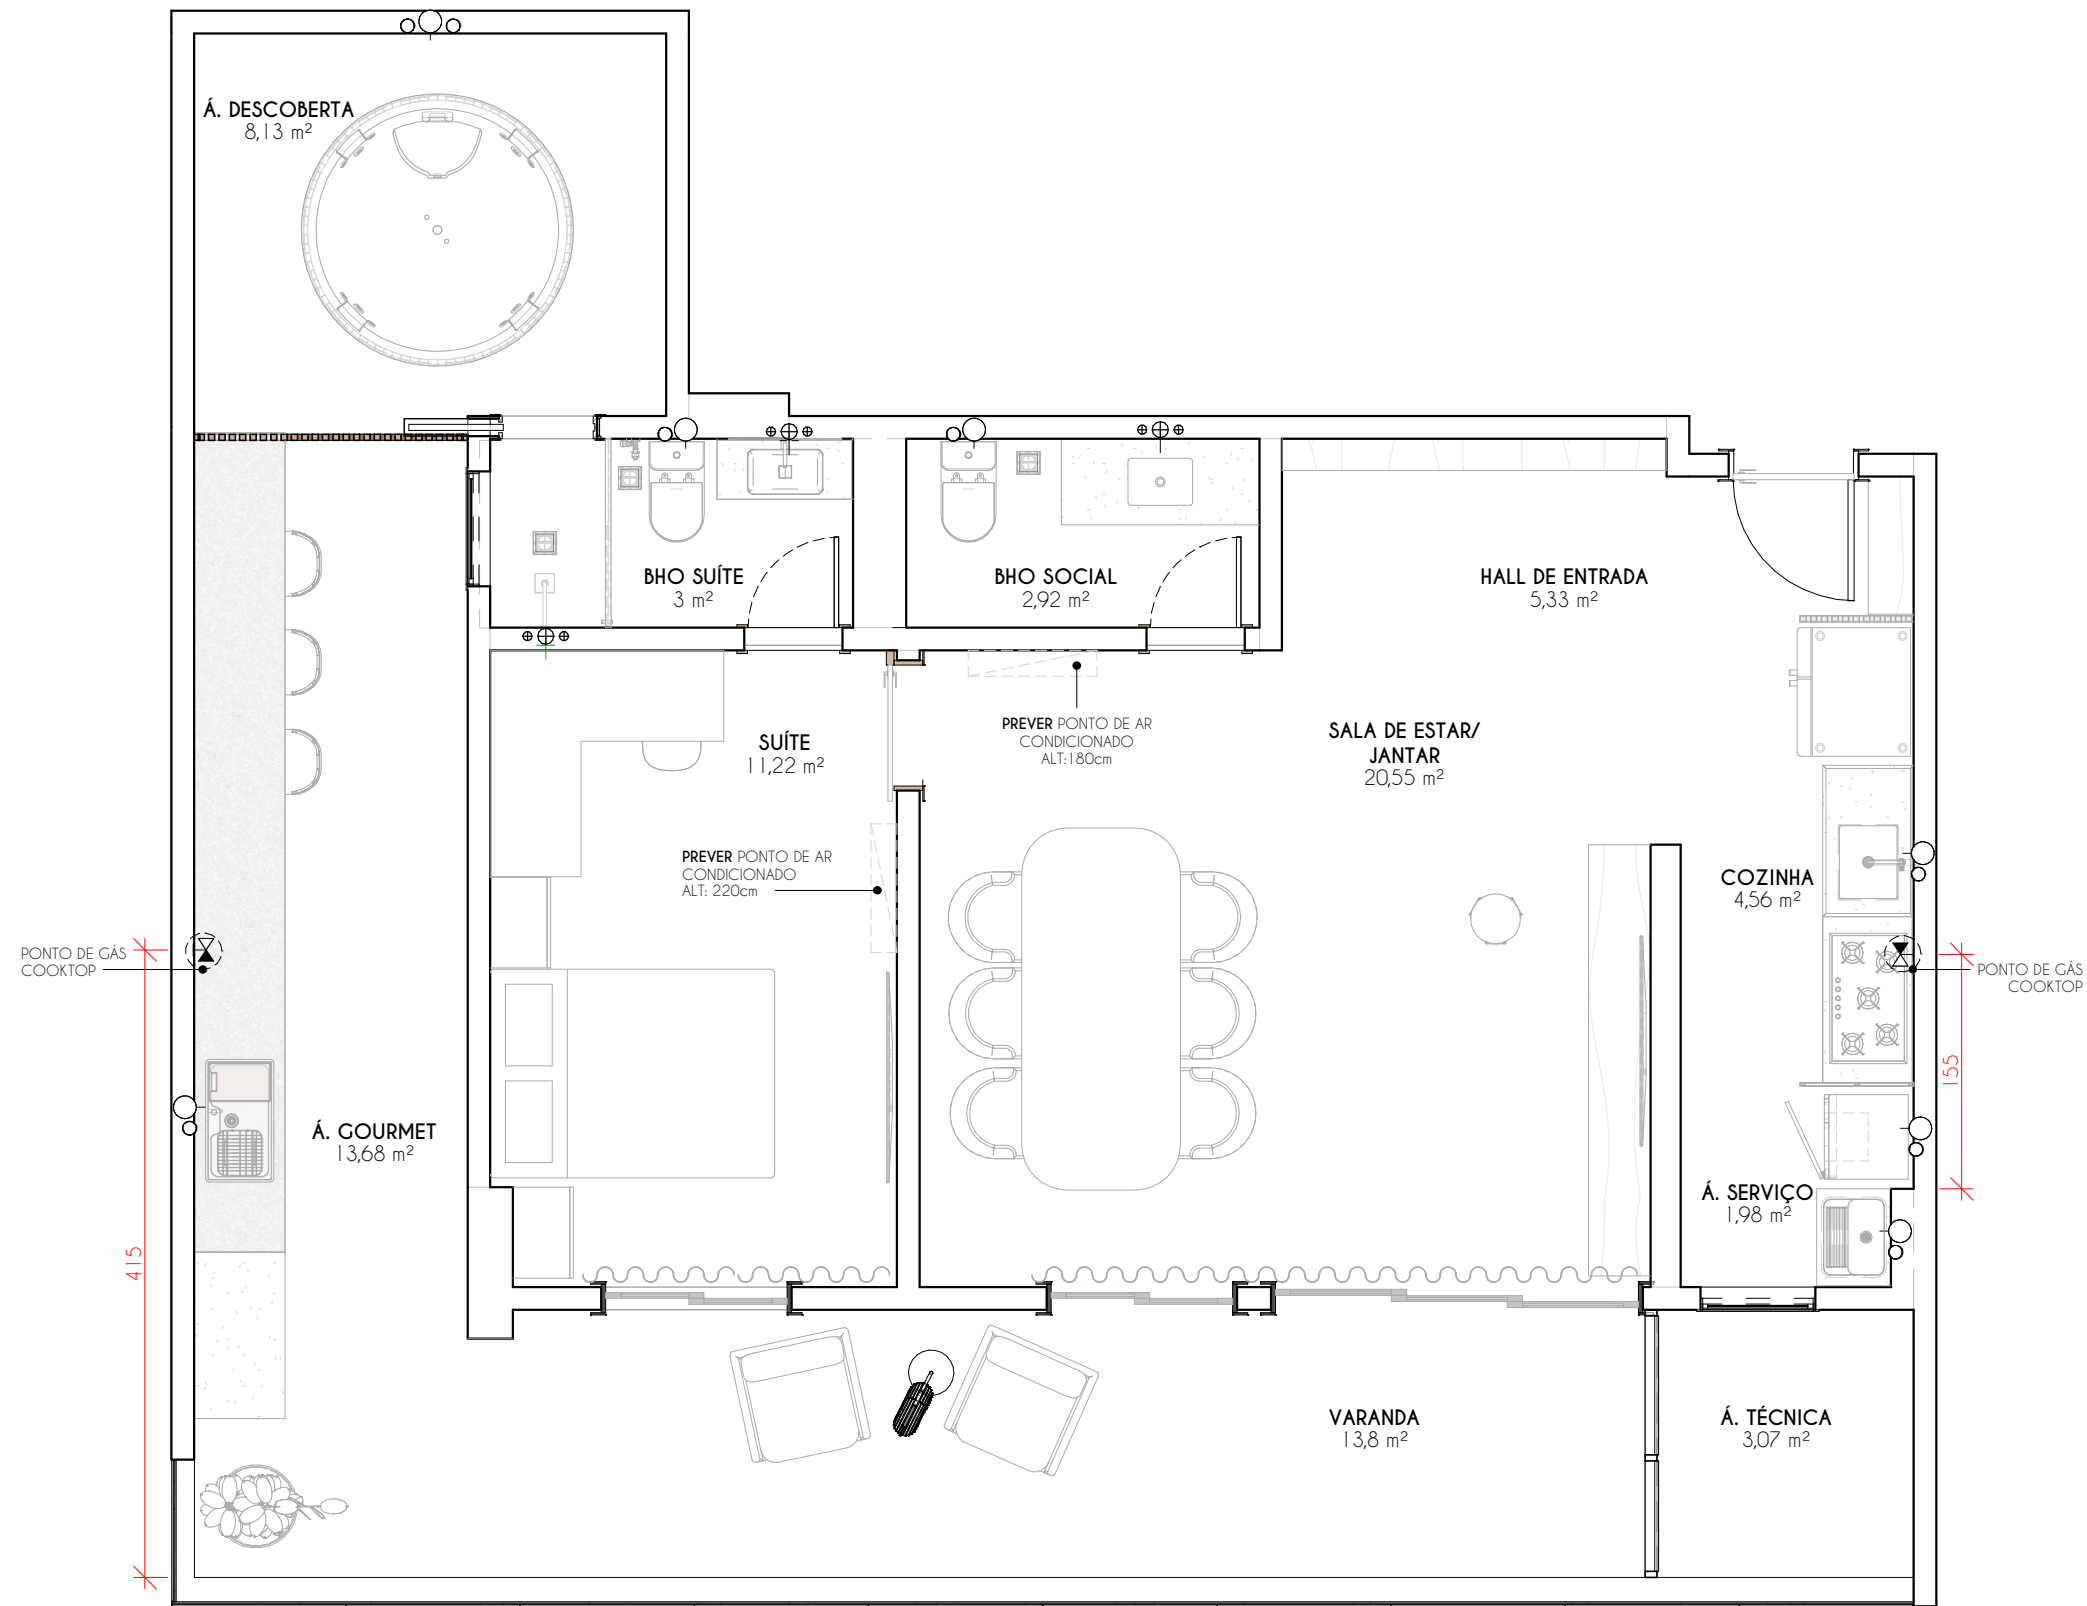

PLANTA BAIXA- PONTOS HIDRÁULICOS

ESCALA 1 : 50

LEGENDA - HIDRÁULICA	
	PTO. REGISTRO DE GÁS
	PTO. ÁGUA FRIA E ESGOTO
	PTO. ÁGUA FRIA, ÁGUA QUENTE E ESGOTO

	MATÉRIA: ARQUITETURA E PLANEJAMENTO DE INTERIORES	TÍTULO: OBRA- PONTOS HIDRÁULICOS, GÁS E AR CONDICIONADO	DATA: JUNHO/2025	PRANCHA: 07.07
	INTEGRANTES: Mariana Gottardo, Emanuely Ferreira e Karolaine Kohler	OBRA: Apartamento Airbnb	ORIENTADO POR: Priscilla Silva Loureiro e Erica Coelho Pagel	