



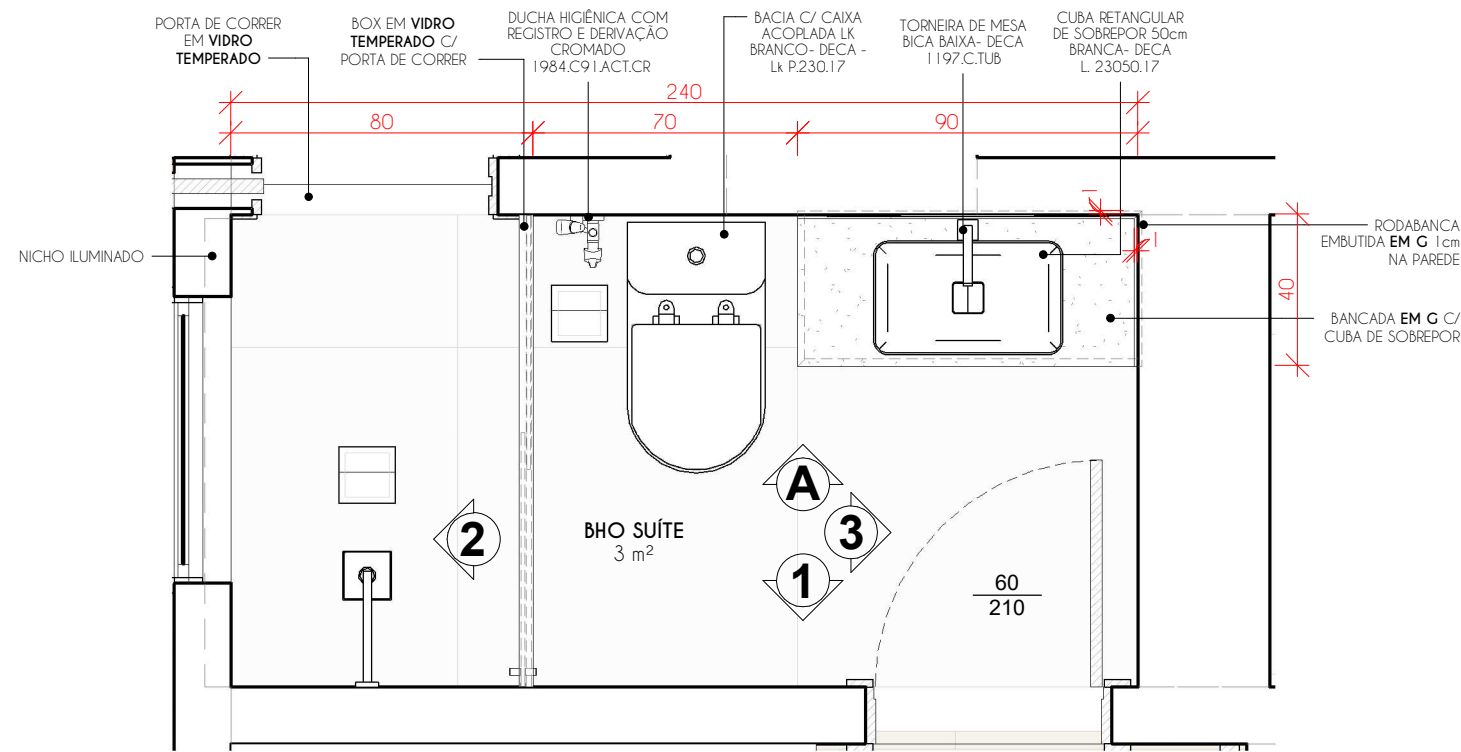


PLANTA BAIXA- AMBIENTAÇÃO

ESCALA 1 : 20

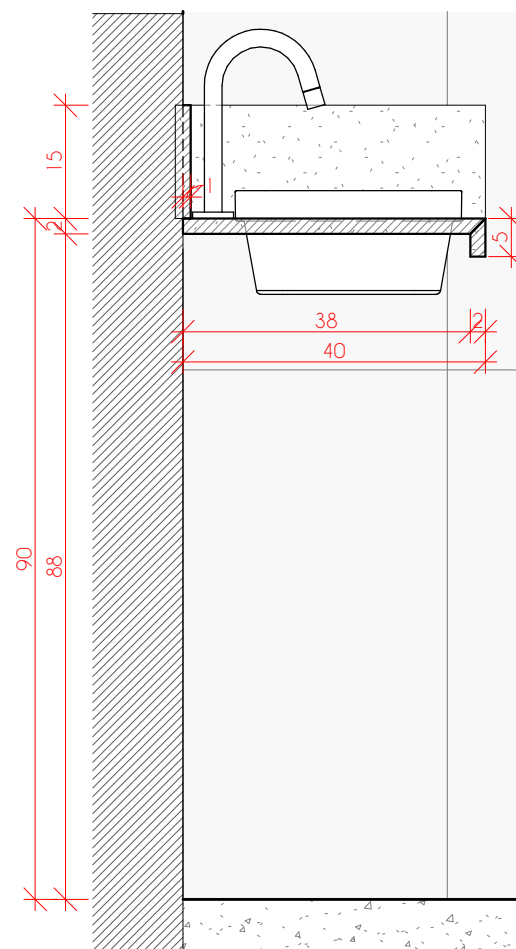

CORTE AA

ESCALA 1 : 10

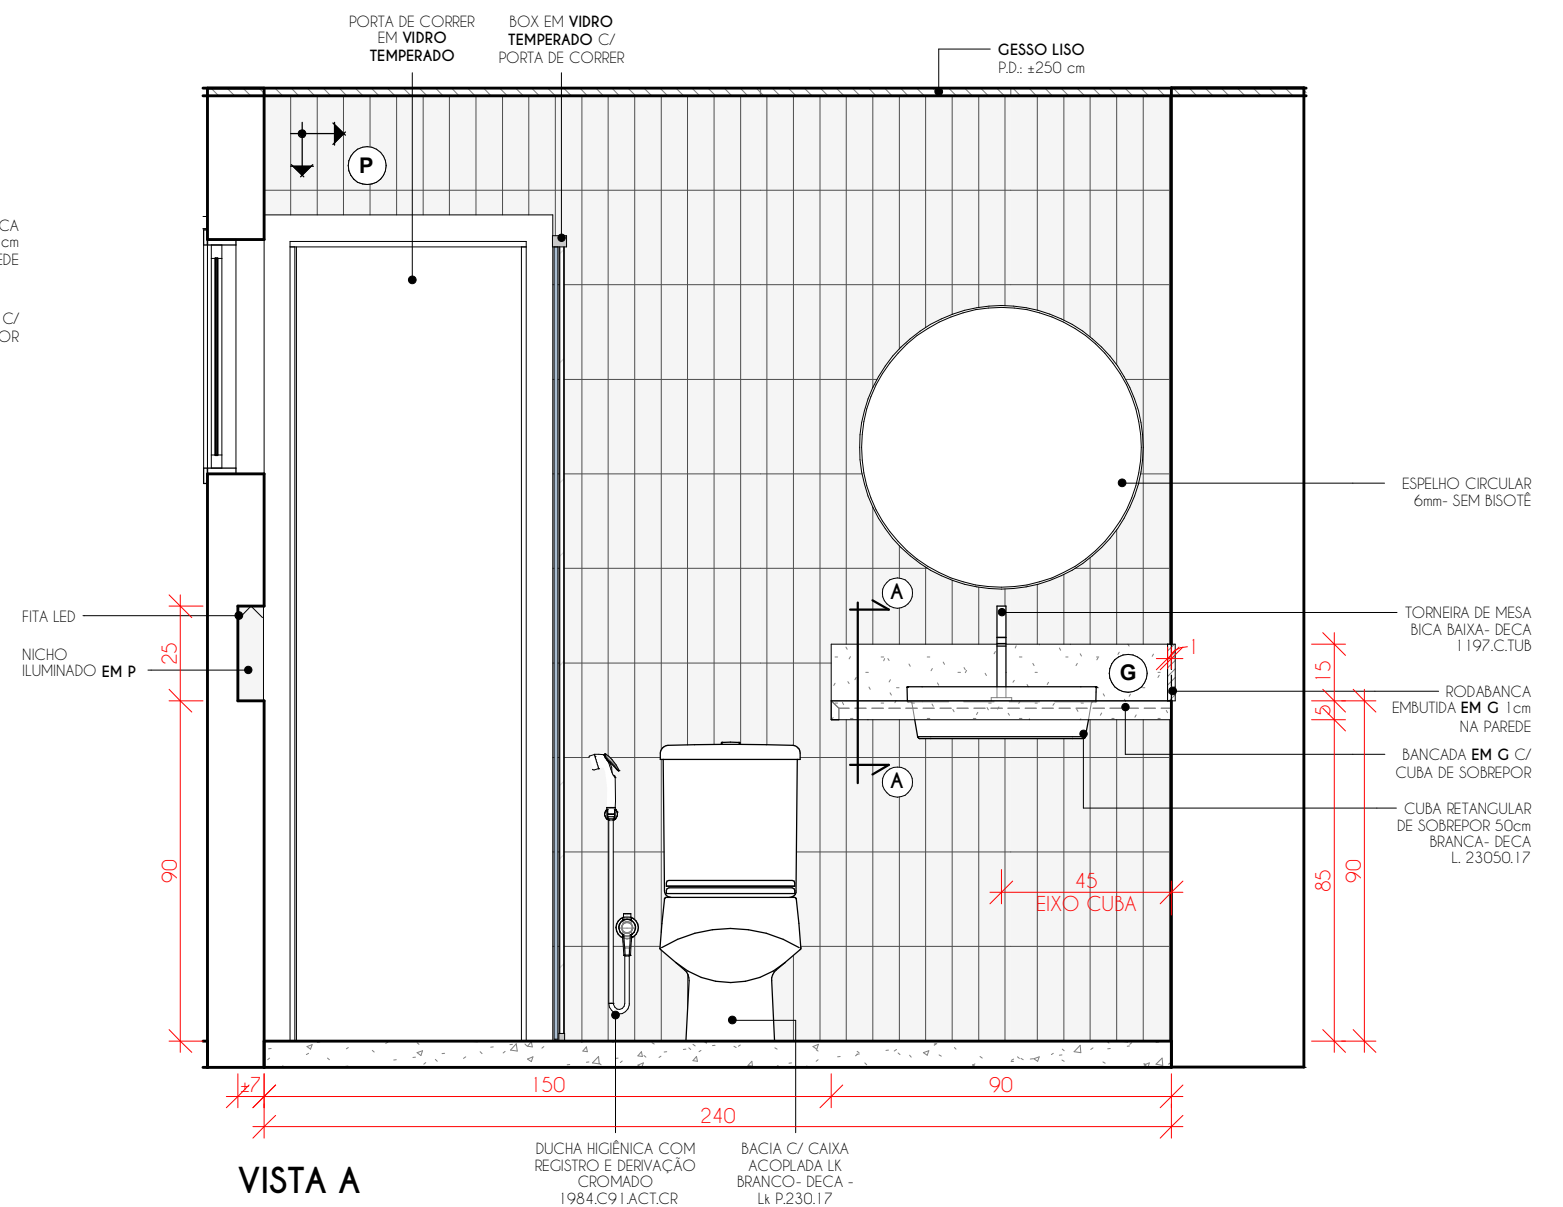

LEGENDA - ESPECIFICAÇÕES

- G** GRANITO PRETO ABSOLUTO ESCOVADO
- M** PORCELANATO CIMENTÍCIO MUNARI BRANCO 90x90- ELIANE
- P** REVESTIMENTO PRISMA HIJAU BR- 07x25

OBS: CONFERIR MEDIDAS NO LOCAL;
TODAS AS QUINAS TERÃO BIZOTE MÍNIMO;
EM CASO DE DÚVIDA CONSULTAR ARQUITETA.



MATÉRIA:
ARQUITETURA E PLANEJAMENTO DE INTERIORES

INTEGRANTES:
Mariana Gottardo, Emanuely Ferreira e Karolaine Kohler

TÍTULO:
DETALHAMENTO- BANHEIRO SUÍTE


OBRA:
Apartamento Airbnb

DATA:
JUNHO/2025


ORIENTADO POR:
Priscilla Silva Loureiro e Erica Coelho Pagel

PRANCHA:


01.02

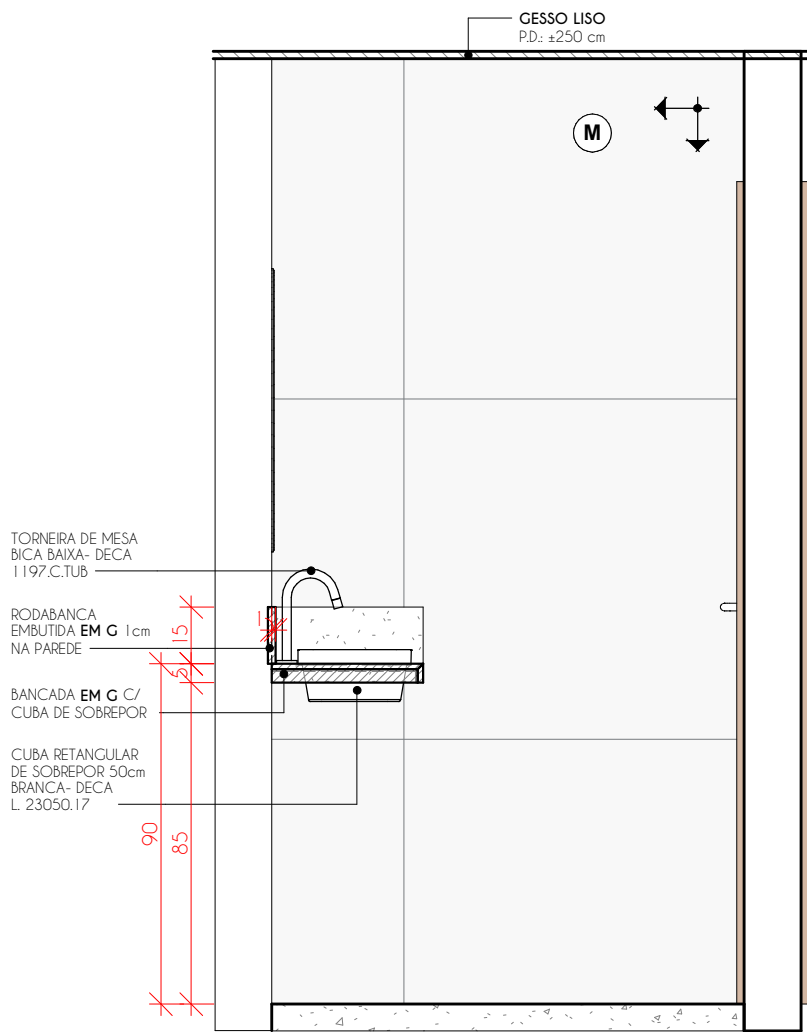


VISTA B
ESCALA 1 : 20

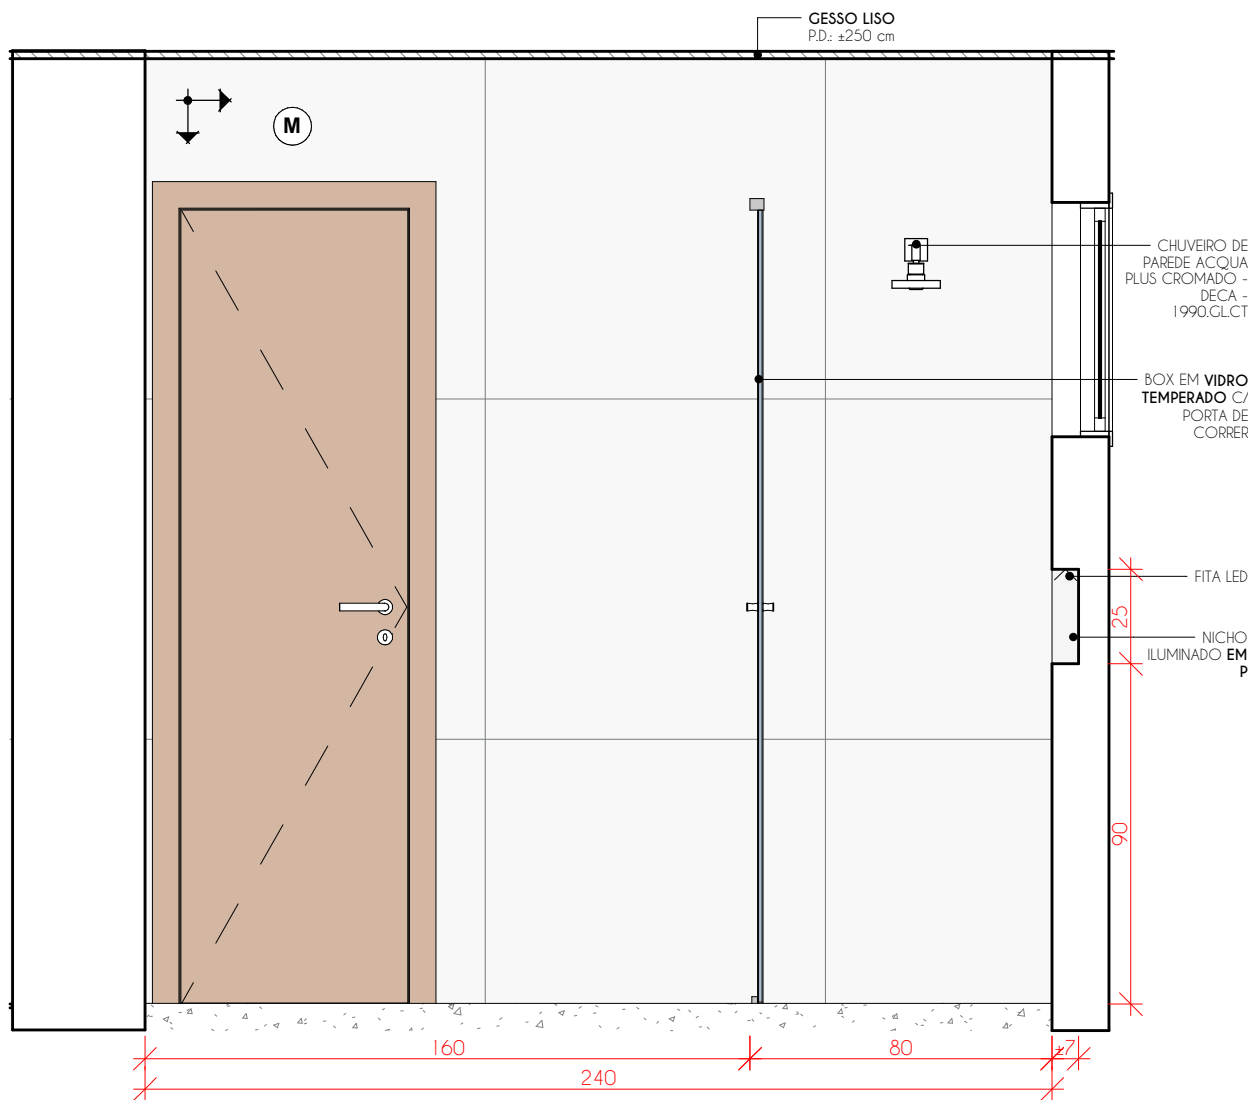

VISTA C
ESCALA 1 : 20

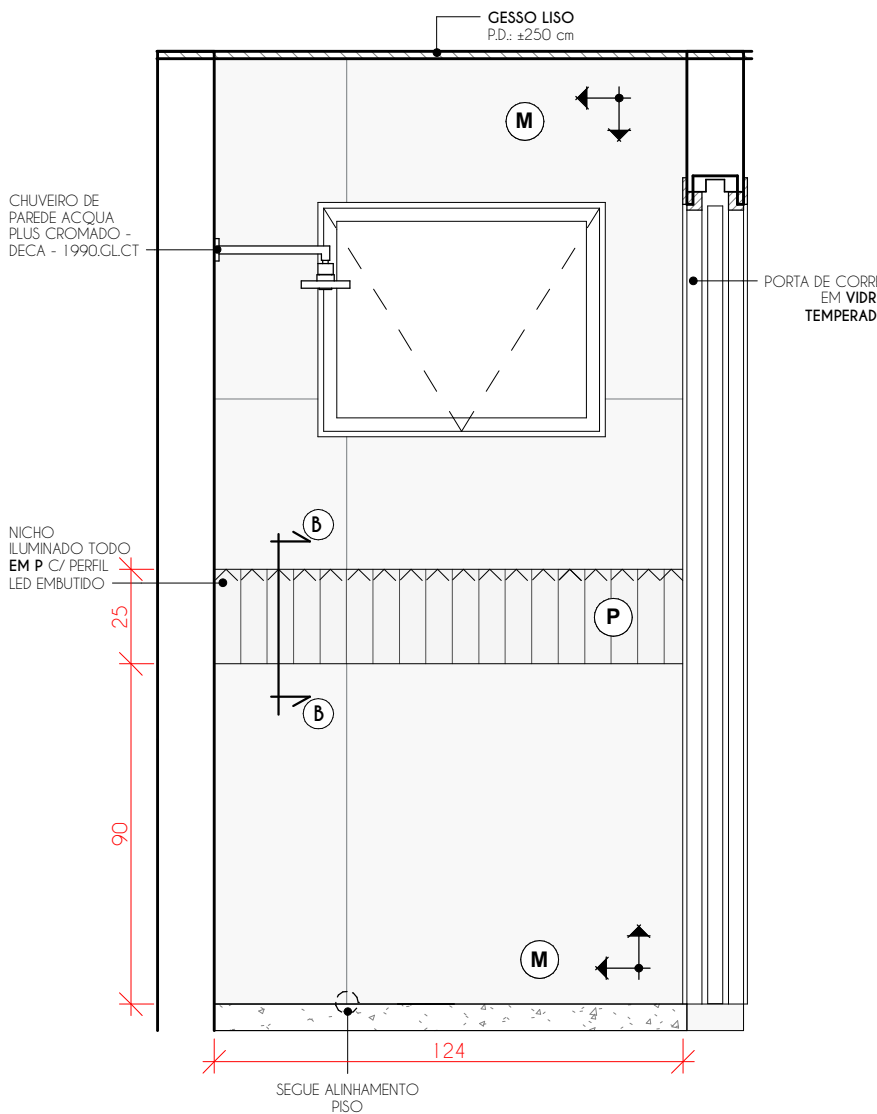

VISTA D
ESCALA 1 : 20

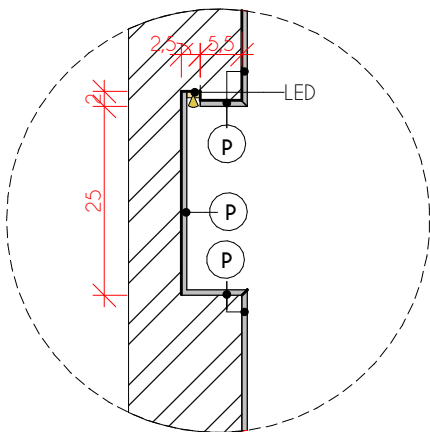

CORTE BB
ESCALA 1 : 10

LEGENDA - ESPECIFICAÇÕES	
G	GRANITO PRETO ABSOLUTO ESCOVADO
M	PORCELANATO CIMENTÍCIO MUNARI BRANCO 90x90- ELIANE
P	REVESTIMENTO PRISMA HIAU BR- 07x25
OBS: CONFERIR MEDIDAS NO LOCAL; TODAS AS QUINAS TERÃO BIZOTE MÍNIMO; EM CASO DE DÚVIDA CONSULTAR ARQUITETA.	

	MATÉRIA: ARQUITETURA E PLANEJAMENTO DE INTERIORES	TÍTULO: DETALHAMENTO- BANHEIRO SUÍTE	DATA: JUNHO/2025	PRANCHA: 02.02
	INTEGRANTES: Mariana Gottardo, Emanuelly Ferreira e Karolaine Kohler	OBRA: Apartamento Airbnb	ORIENTADO POR: Priscilla Silva Loureiro e Erica Coelho Pagel	