






	MATÉRIA:	TÍTULO:	DATA:	PRANCHA: 01.02
	ARQUITETURA E PLANEJAMENTO DE INTERIORES INTEGRANTES: Mariana Gottardo, Emanuely Ferreira e Karolaine Kohler	DETALHAMENTO- COZINHA OBRA: Apartamento Airbnb	JUNHO/2025 ORIENTADO POR: Priscilla Silva Loureiro e Erica Coêlho Pagel	

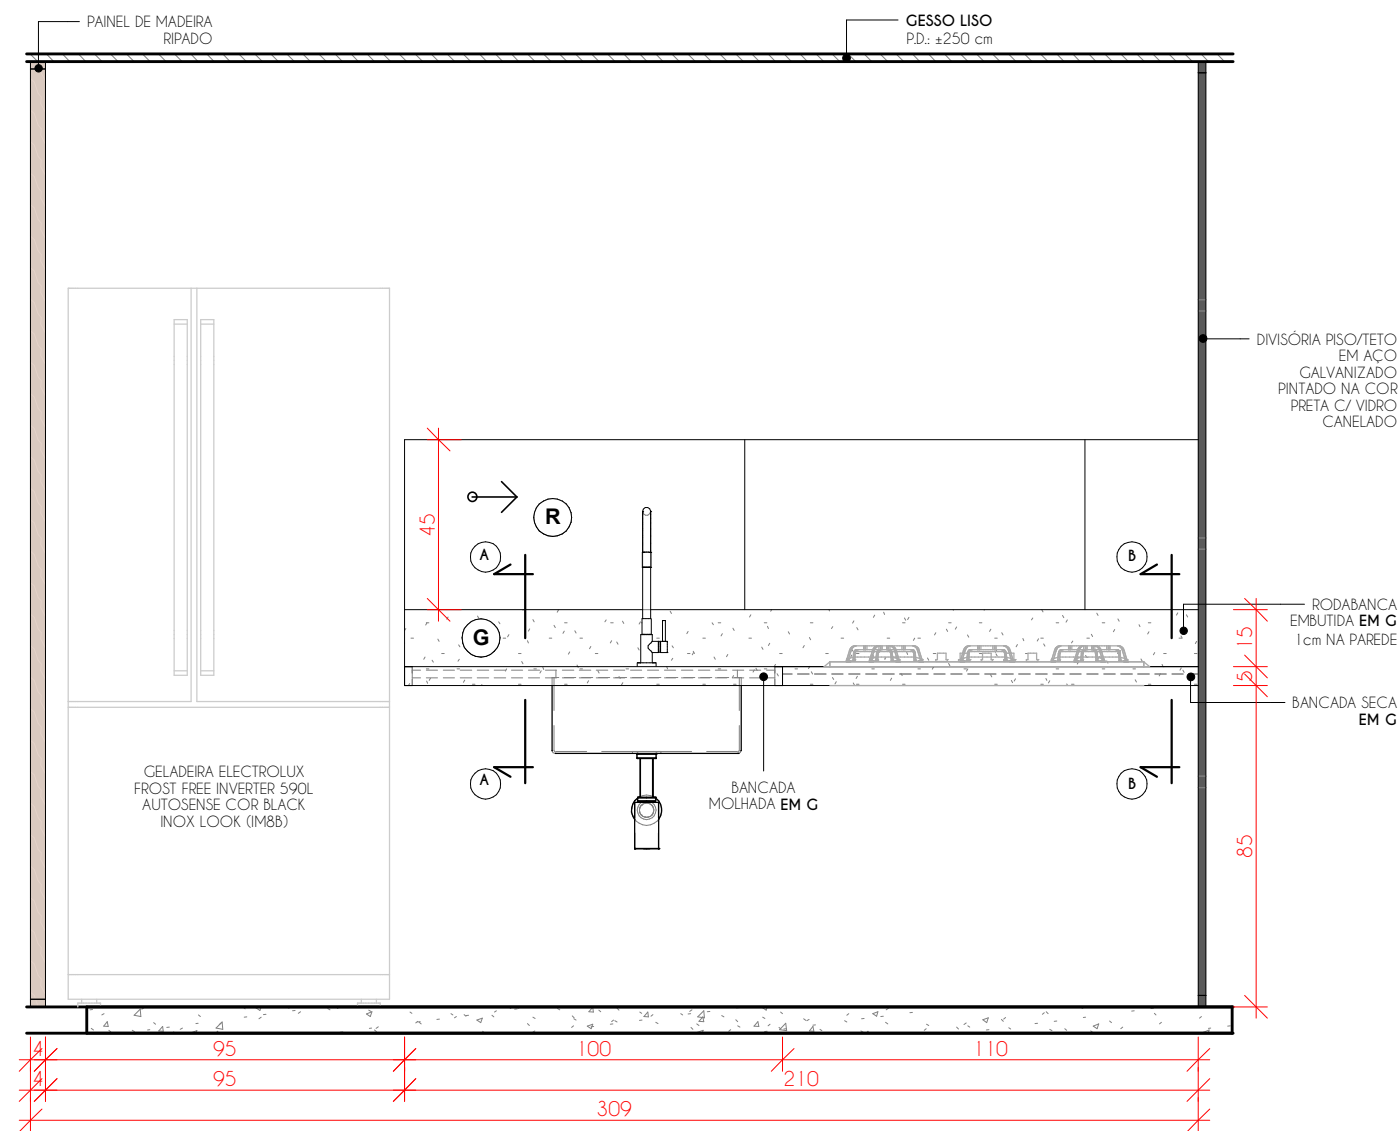

VISTA B
ESCALA 1 : 20

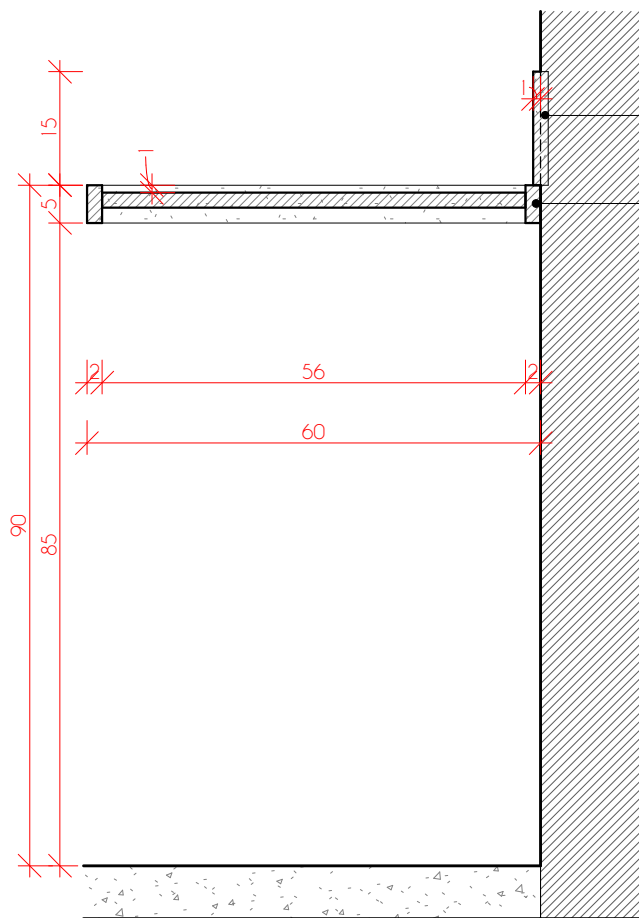

CORTE AA
ESCALA 1 : 10

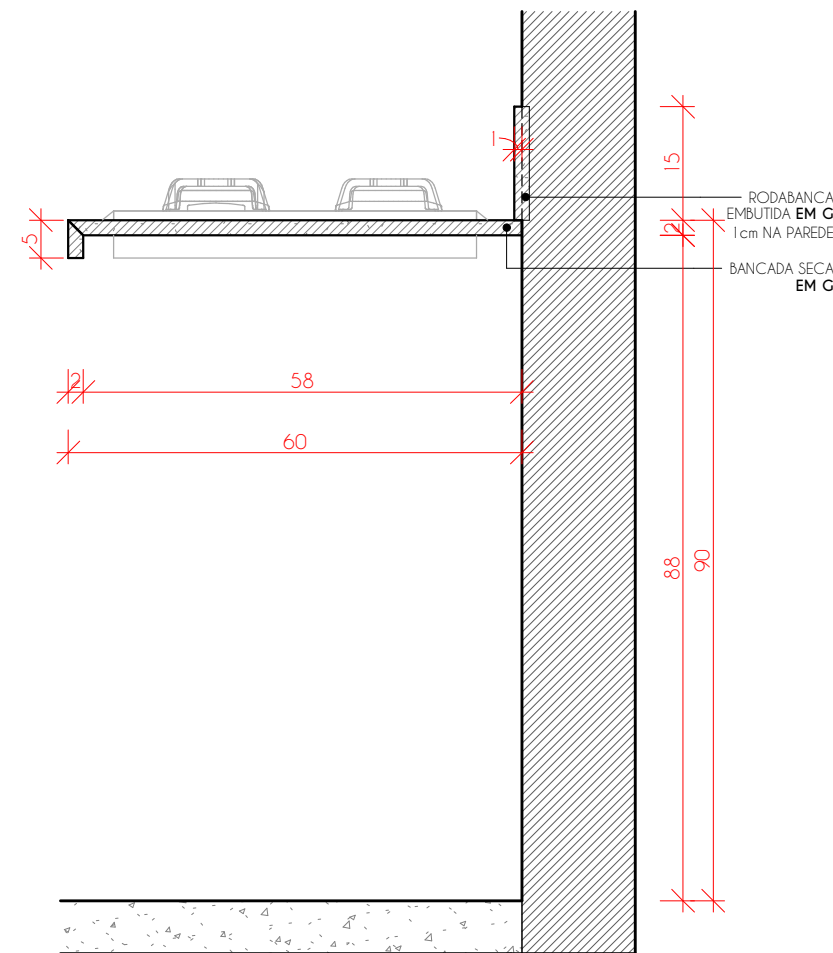

CORTE BB
ESCALA 1 : 10

LEGENDA - ESPECIFICAÇÕES

- (R) PORCELANATO RIG BIANCO ACETINADO- 45x90 cm - RET. - BIANCOGRES
(C) GRANITO PRETO ABSOLUTO

OBS: CONFERIR MEDIDAS NO LOCAL;
TODAS AS QUINAS TERÃO BIZOTE MÍNIMO;
EM CASO DE DÚVIDA CONSULTAR ARQUITETA.



MATÉRIA:
ARQUITETURA E PLANEJAMENTO DE INTERIORES
INTEGRANTES:
Mariana Gottardo, Emanuely Ferreira e Karolaine Kohler

TÍTULO:
DETALHAMENTO- COZINHA
OBRA:
Apartamento Airbnb

DATA:
JUNHO/2025
ORIENTADO POR:
Priscilla Silva Loureiro e Erica Coelho Pagel

PRANCHA:
02.02