





PLANTA BAIXA - APARTAMENTOS
ESC: 1 : 100

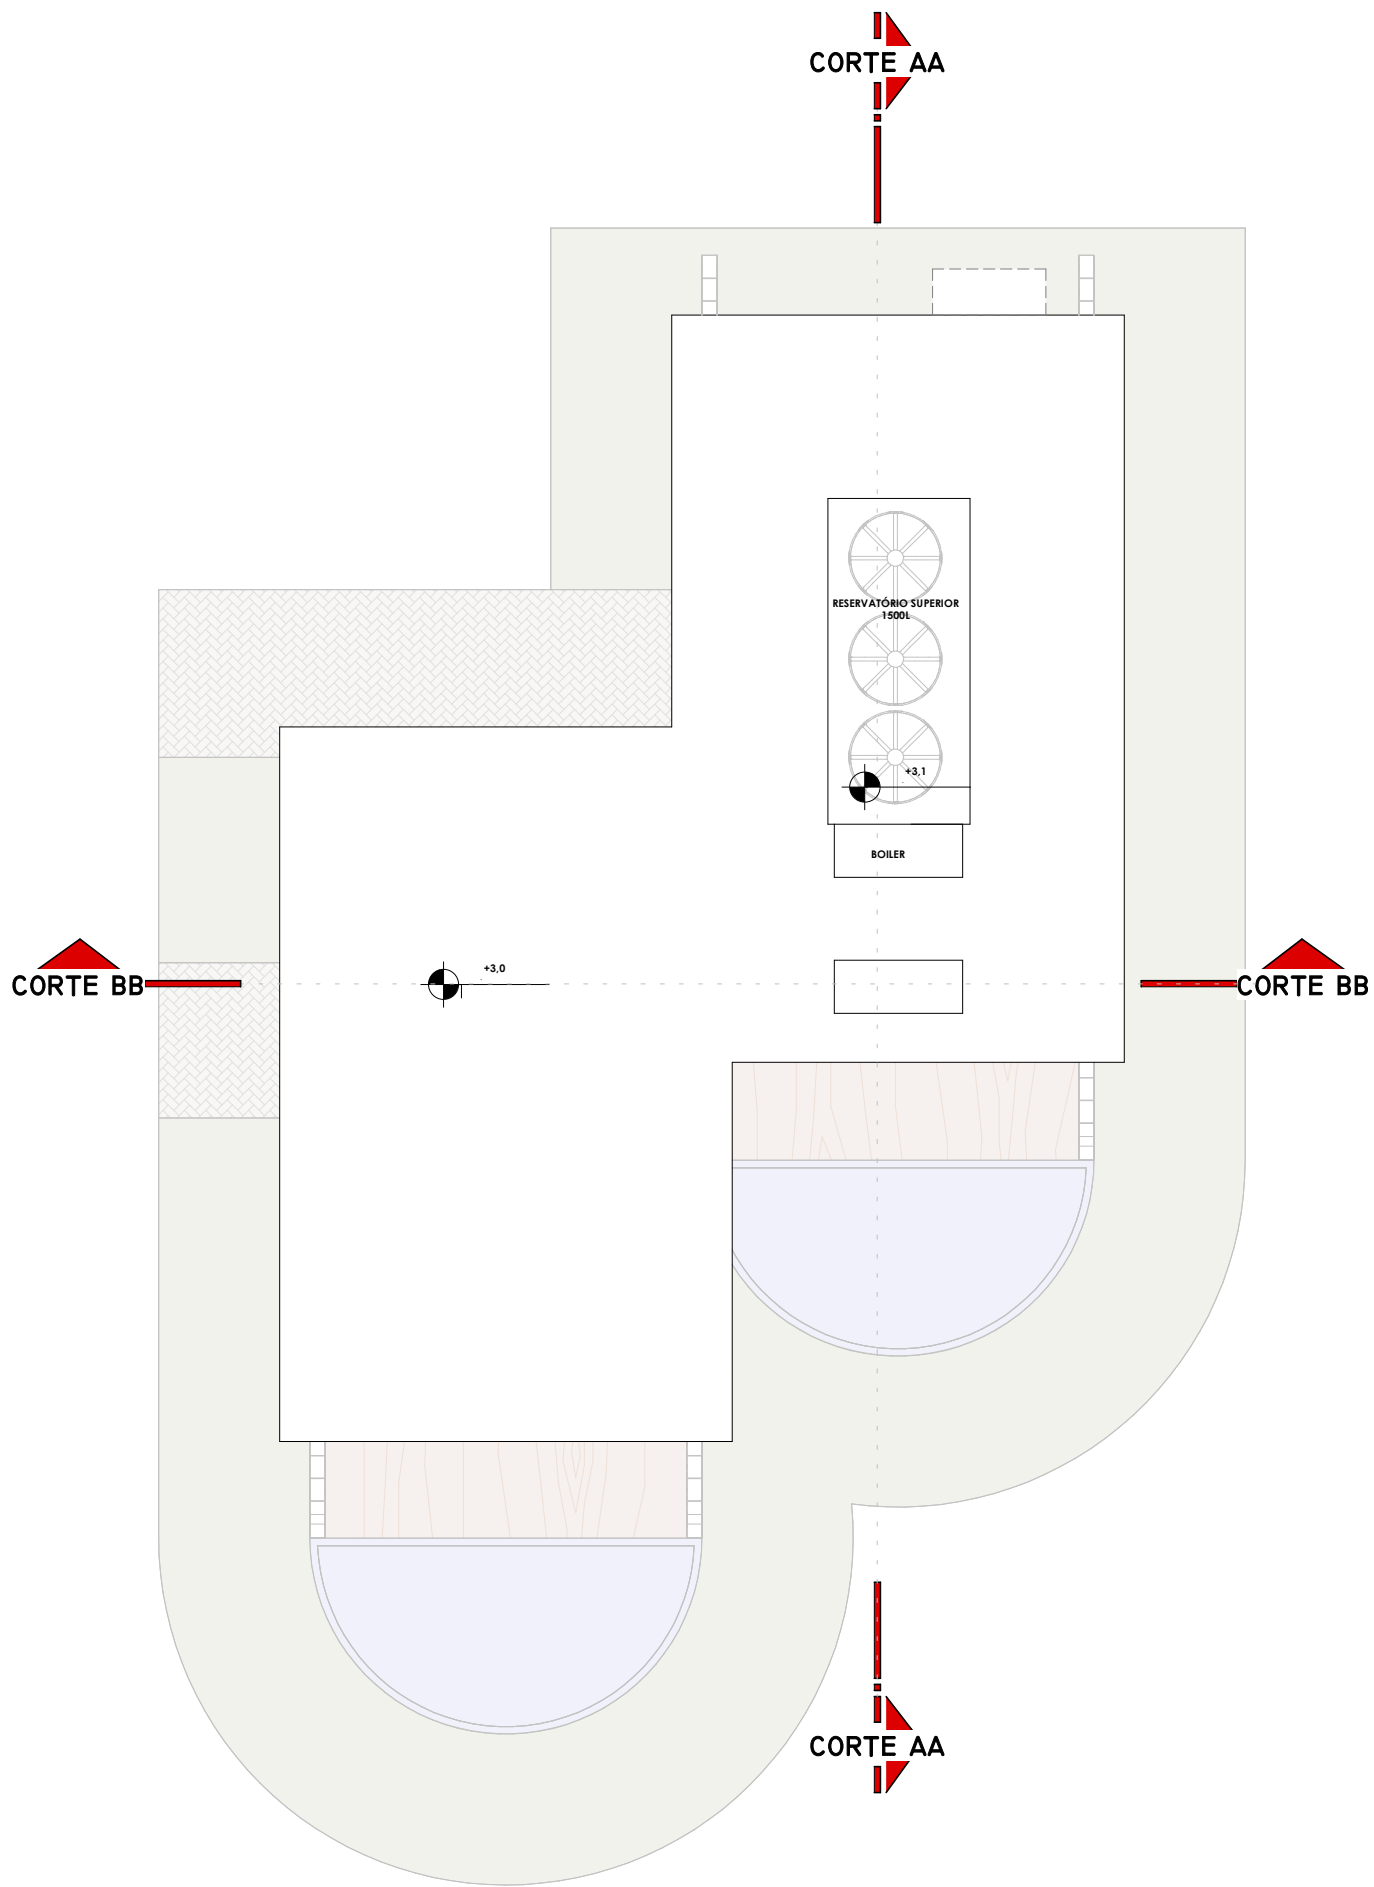


PLANTA DE COBERTURA - APARTAMENTOS
ESC: 1 : 100

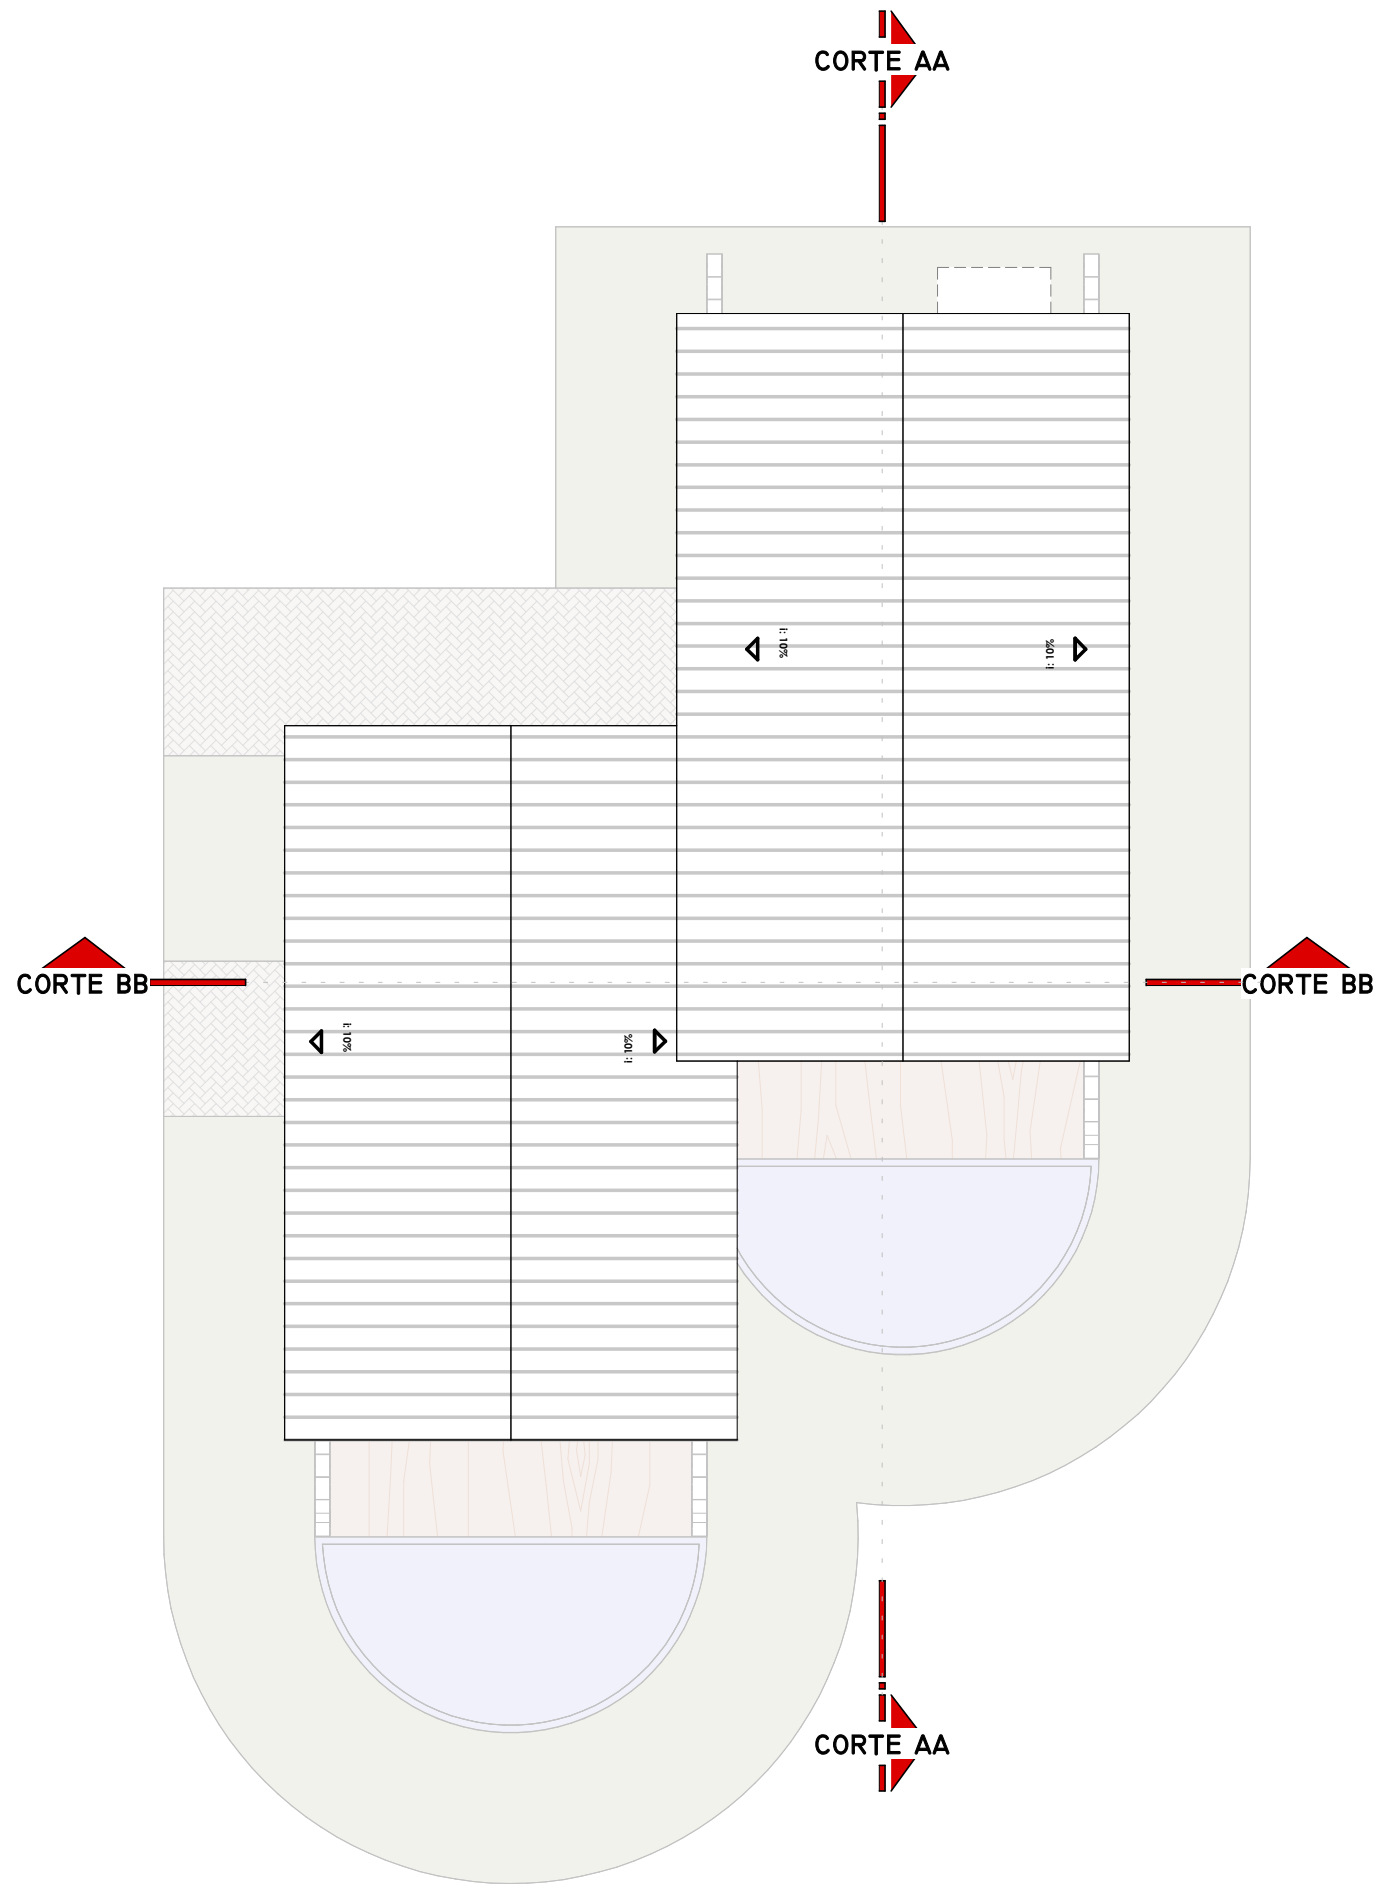

PLANTA DE COBERTURA - APARTAMENTOS
ESC: 1 : 100




CORTE BB - APARTAMENTO
ESC: 1 : 100

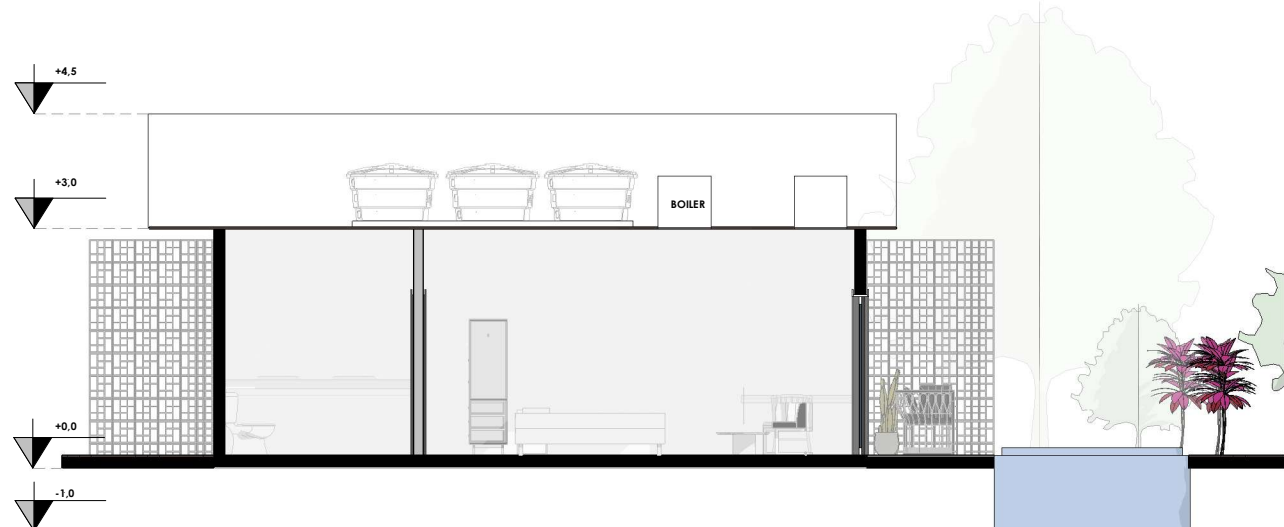


CORTE AA - APARTAMENTO
ESC: 1 : 100



IMPLANTAÇÃO

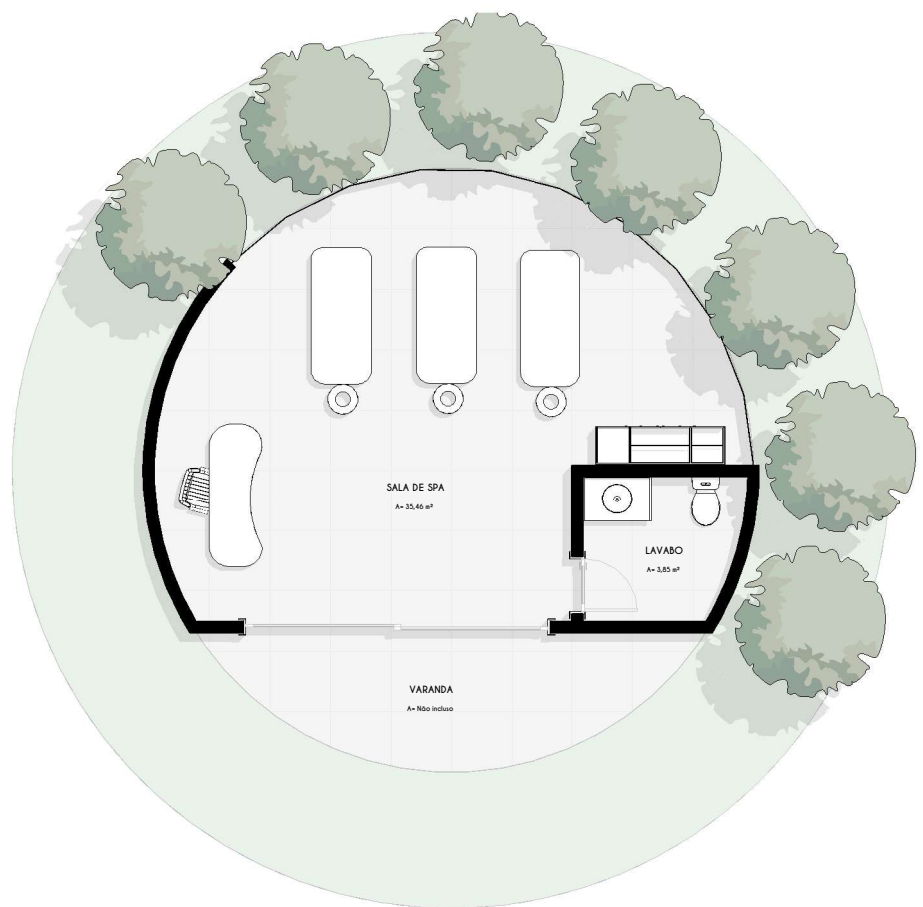

PLANTA BAIXA - SPA
ESC: 1 : 100

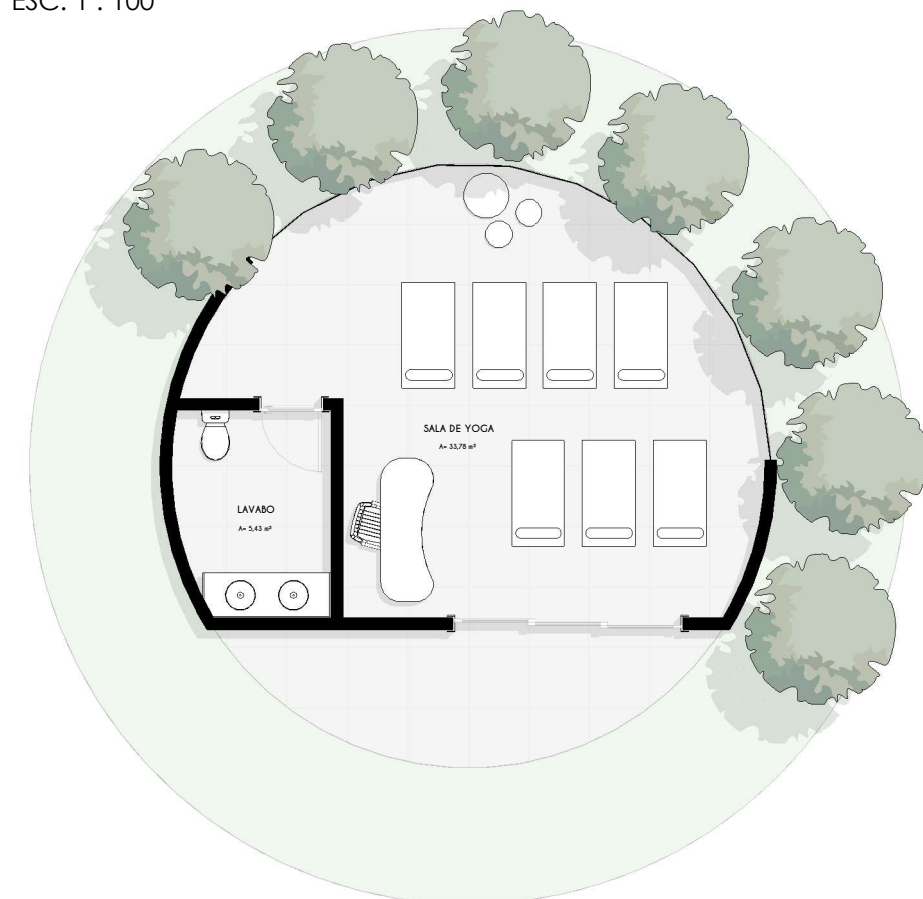

PLANTA BAIXA - SALA DE YOGA
ESC: 1 : 100

QUADRO DE JANELAS				
Cód.	Dimensões	Área	Quantidade	
	Largura	Altura		
J31	200 cm	150 cm	3,00 m²	3
J34	75 cm	60 cm	0,45 m²	1
J35	100 cm	60 cm	0,60 m²	1
J36	35 cm	60 cm	0,33 m²	9
J39	175 cm	150 cm	2,63 m²	2
J40	240 cm	150 cm	3,60 m²	2
J41	100 cm	60 cm	0,60 m²	5
J42	100 cm	60 cm	0,60 m²	1
			24	

QUADRO DE PORTAS				
Cód.	Dimensões	Área	Quantidade	
	Largura	Altura		
P02	140 cm	210 cm	2,94 m²	2
P04	240 cm	270 cm	6,48 m²	3
P05	300 cm	210 cm	6,30 m²	3
P06	<varia>	210 cm	<varia>	4
P07	250 cm	210 cm	5,25 m²	1
P13	80 cm	210 cm	1,68 m²	9
P15	70 cm	210 cm	1,47 m²	1
P16	70 cm	210 cm	1,47 m²	3
P17	80 cm	210 cm	1,68 m²	9
P21	80 cm	210 cm	1,68 m²	9
P22	90 cm	210 cm	1,89 m²	6
P25	90 cm	210 cm	1,89 m²	2
P28	60 cm	210 cm	1,26 m²	8
P30	70 cm	210 cm	1,47 m²	3
P31	90 cm	210 cm	1,89 m²	2
P32	100 cm	210 cm	2,10 m²	4
P42	90 cm	210 cm	1,89 m²	1
P48	100 cm	210 cm	2,10 m²	28
P49	140 cm	210 cm	2,94 m²	2
P52	160 cm	210 cm	3,36 m²	5
P54	140 cm	210 cm	2,94 m²	1
P57	400 cm	240 cm	9,60 m²	2
			108	

SETORIZAÇÃO

- | | | | |
|---|------------------------|----|----------------------|
| 1 | LOBBY E ADMINISTRATIVO | 8 | QUADRA POLIESP. |
| 2 | LOJA | 9 | RESTAUR. / CAFETERIA |
| 3 | SERVIÇO | 10 | QUADRA VOLÊI |
| 4 | BAR | 11 | GOLF |
| 5 | RESTAURANTE- HÓSPEDES | 12 | SPA |
| 6 | APARTAMENTOS | 13 | YOGA / PILATES |
| 7 | BANGALÔS | 14 | PISCINA AQUECIDA |


ATELIÉ IV - RESORT SOLARA

ORIENTADO POR:
CLÓVIS AQUINO, LARISSA ANDARA,
PRISCILA LOUREIRO


PROJETADO POR:
EMANUELY FERREIRA, KAROLAINA KOHLER
E MARIANA GOTTARDO

PRANCHA:

01/01

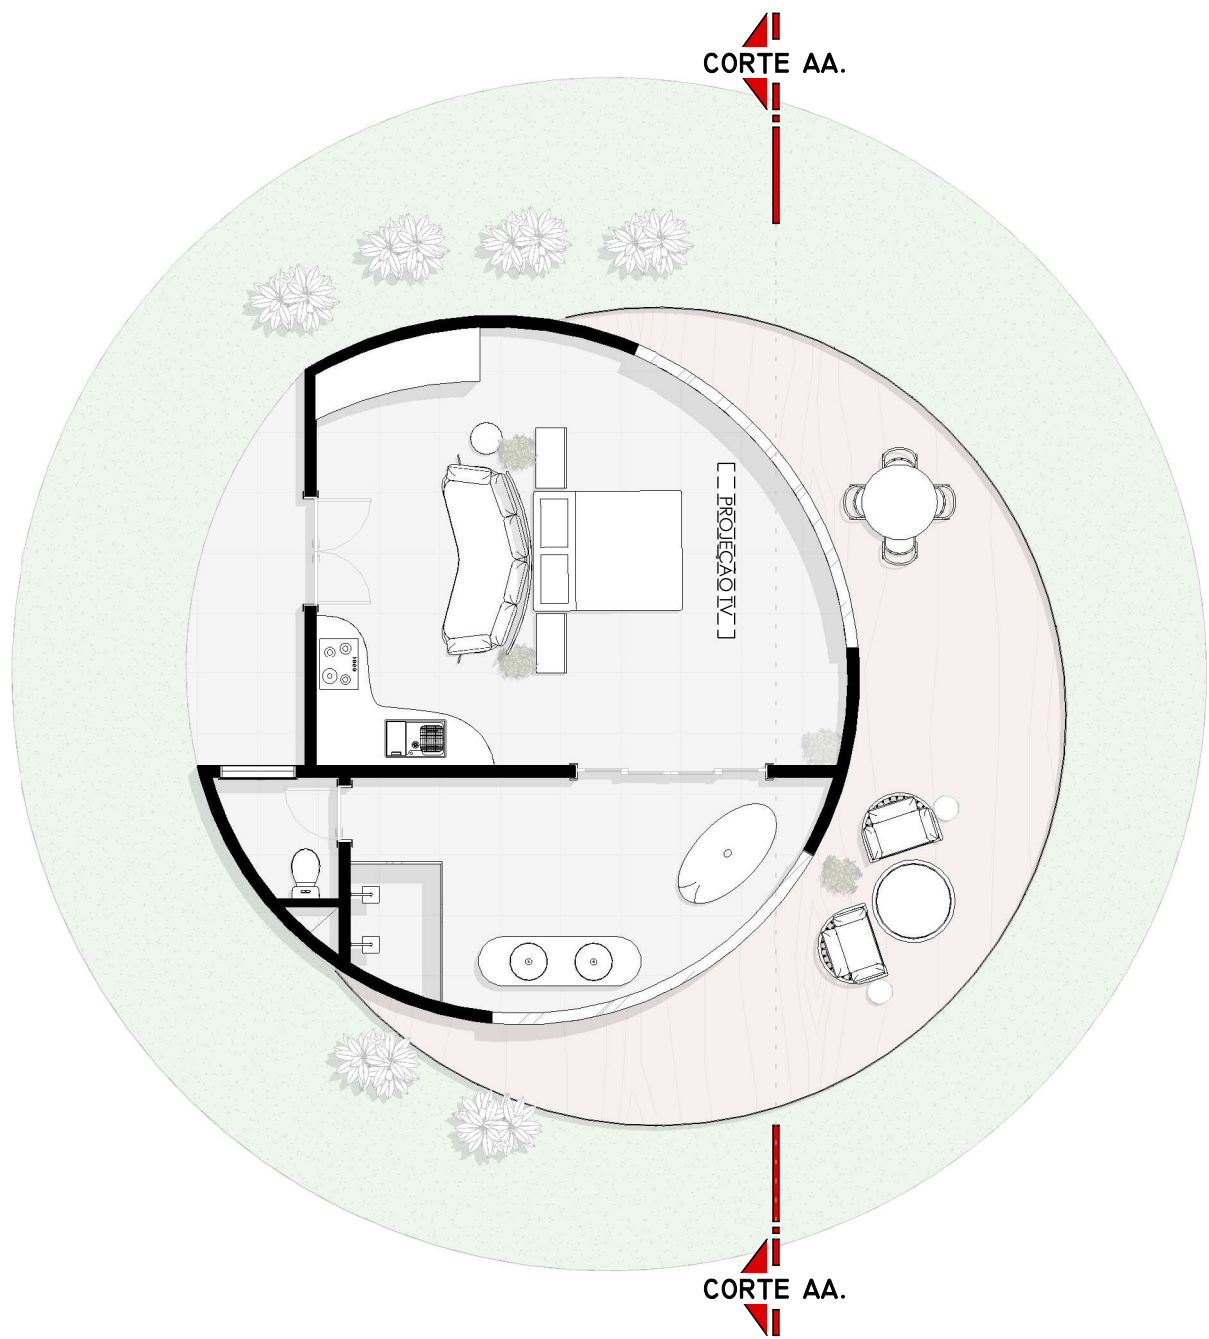


PLANTA BAIXA - BANGALÔ
ESC: 1 : 100

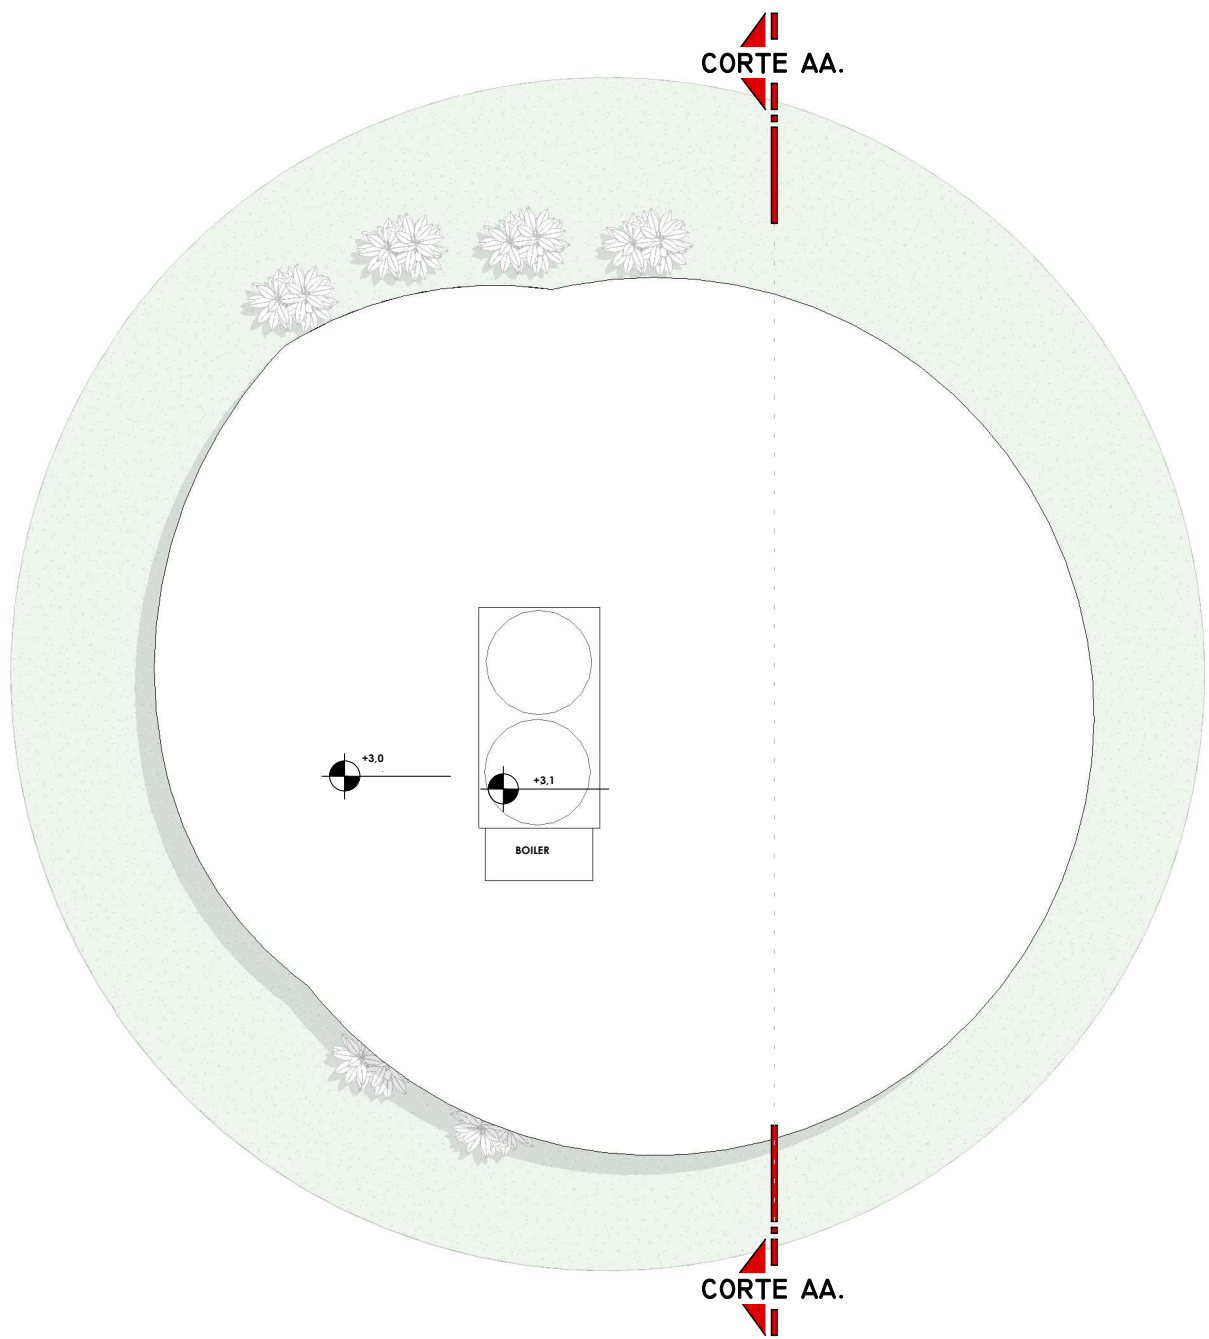

PLANTA DE COBERTURA - BANGALÔ
ESC: 1 : 100




IMPLANTAÇÃO

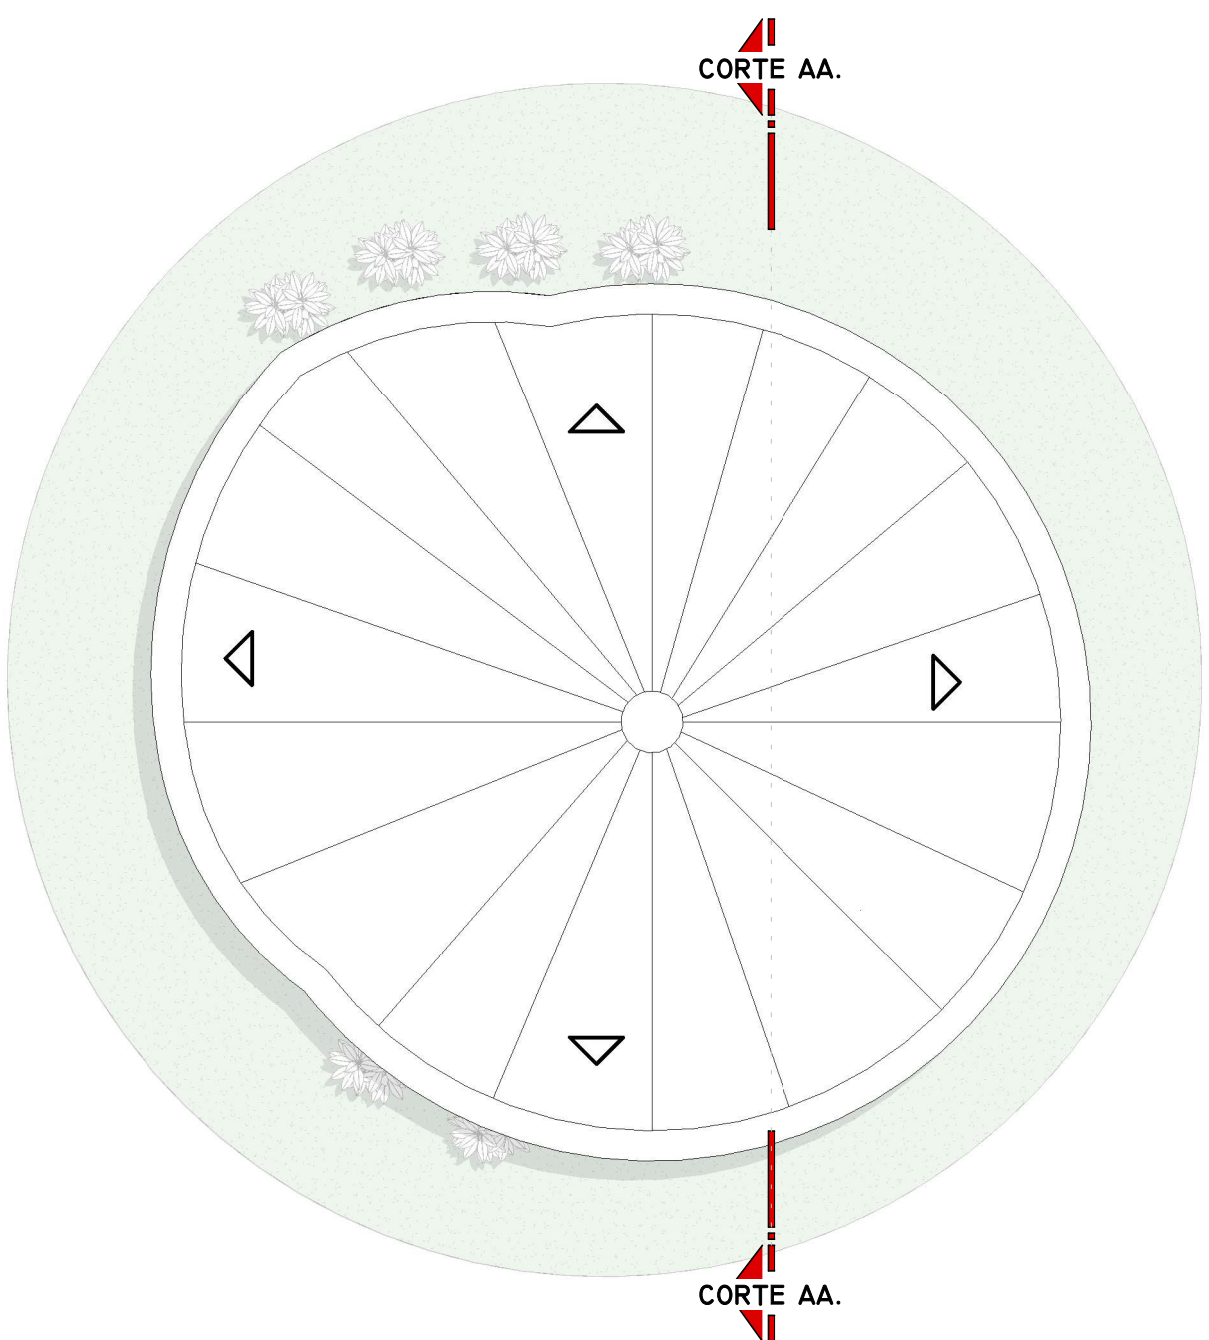

PLANTA DE COBERTURA - BANGALÔ
ESC: 1 : 100



CORTE AA - BANGALÔ
ESC: 1 : 100

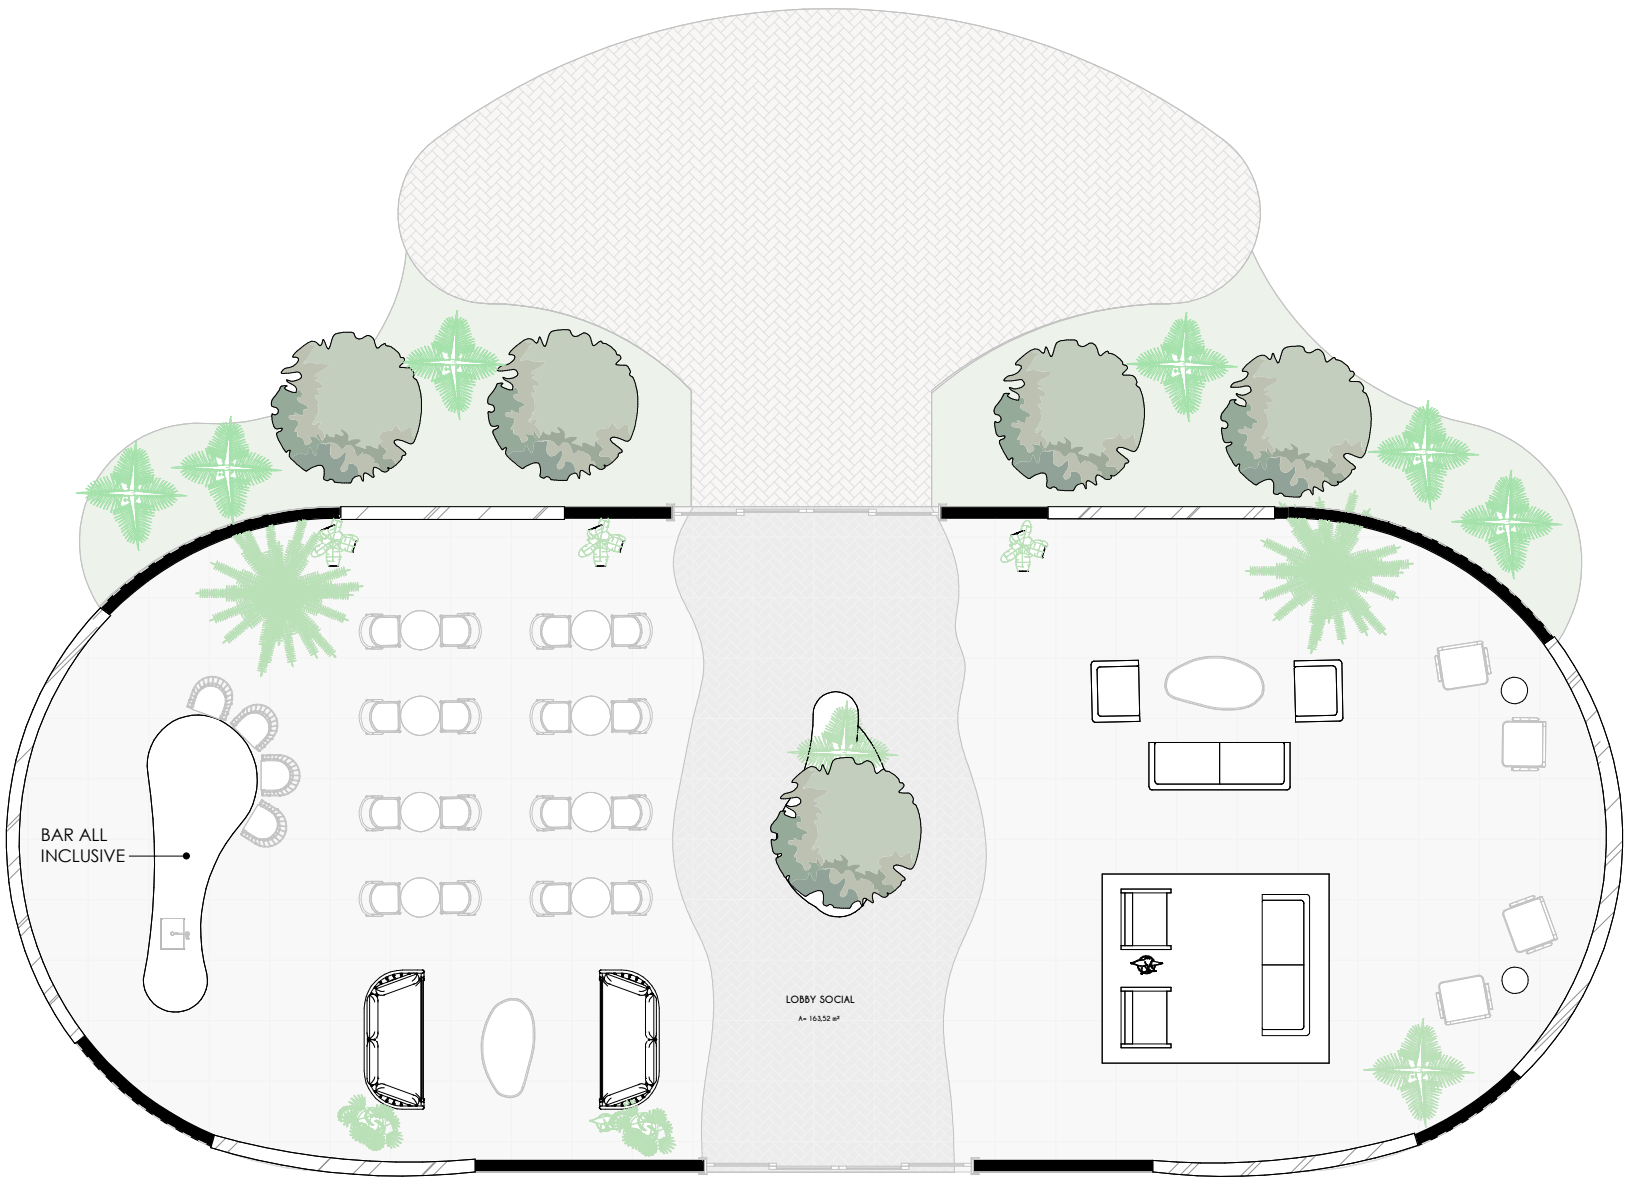

PLANTA BAIXA - ÁREA DE VIVÊNCIA
ESC: 1 : 100

QUADRO DE JANELAS				
Cód.	Dimensões		Quantidade	
	Largura	Altura		
J31	200 cm	150 cm	3	
J34	75 cm	60 cm	1	
J35	100 cm	60 cm	1	
J36	55 cm	60 cm	9	
J39	175 cm	150 cm	2	
J40	240 cm	150 cm	2	
J41	100 cm	60 cm	5	
J42	100 cm	60 cm	1	

QUADRO DE PORTAS				
Cód.	Dimensões		Área	Quant.
	Largura	Altura		
P02	140 cm	210 cm	2,94 m²	2
P04	240 cm	270 cm	6,48 m²	3
P05	300 cm	210 cm	6,30 m²	3
P06	<varia>	210 cm	<varia>	4
P07	250 cm	210 cm	5,25 m²	1
P13	80 cm	210 cm	1,68 m²	9
P15	70 cm	210 cm	1,47 m²	1
P16	70 cm	210 cm	1,47 m²	3
P17	80 cm	210 cm	1,68 m²	9
P21	80 cm	210 cm	1,68 m²	9
P22	90 cm	210 cm	1,89 m²	6
P25	90 cm	210 cm	1,89 m²	2
P28	60 cm	210 cm	1,26 m²	8
P30	70 cm	210 cm	1,47 m²	3
P31	90 cm	210 cm	1,89 m²	2
P32	100 cm	210 cm	2,10 m²	4
P42	90 cm	210 cm	1,89 m²	1
P48	100 cm	210 cm	2,10 m²	28
P49	140 cm	210 cm	2,94 m²	2
P52	160 cm	210 cm	3,36 m²	5
P54	140 cm	210 cm	2,94 m²	1
P57	400 cm	240 cm	9,60 m²	2

SETORIZAÇÃO

- | | |
|--------------------------|------------------------|
| 1 LOBBY E ADMINISTRATIVO | 8 QUADRA POLIESP. |
| 2 LOJA | 9 RESTAUR. / CAFETERIA |
| 3 SERVIÇO | 10 QUADRA VOLÊI |
| 4 BAR | 11 GOLF |
| 5 RESTAURANTE- HÓSPEDES | 12 SPA |
| 6 APARTAMENTOS | 13 YOGA / PILATES |
| 7 BANGALÔS | 14 PISCINA AQUECIDA |

ATELIÉ IV - RESORT SOLARA

ORIENTADO POR:

CLOVIS AQUINO, LARISSA ANDARA,
PRISCILA LOUREIRO

PROJETADO POR:

EMANUELY FERREIRA, KAROLINE KOHLER
E MARIANA GOTTARDO

PRANCHA:

01/01



QUADRO DE JANELAS

Cód.	Dimensões			Quantidade	P28	60 cm	210 cm	1,26 m²	8
	Largura	Altura	Área		P30	70 cm	210 cm	1,47 m²	3
J31	200 cm	150 cm	3,00 m²	3	P31	90 cm	210 cm	1,89 m²	2
J34	75 cm	60 cm	0,45 m²	1	P32	100 cm	210 cm	2,10 m²	4
J35	100 cm	60 cm	0,60 m²	1	P42	90 cm	210 cm	1,89 m²	1
J36	55 cm	60 cm	0,33 m²	9	P48	100 cm	210 cm	2,10 m²	28
J39	175 cm	150 cm	2,63 m²	2	P49	140 cm	210 cm	2,94 m²	2
J40	240 cm	150 cm	3,60 m²	2	P52	160 cm	210 cm	3,36 m²	5
J41	100 cm	60 cm	0,60 m²	5	P54	140 cm	210 cm	2,94 m²	1
J42	100 cm	60 cm	0,60 m²	1	P57	400 cm	240 cm	9,60 m²	2
				24					
									108

SETORIZAÇÃO

- | | | | |
|---|------------------------|----|----------------------|
| 1 | LOBBY E ADMINISTRATIVO | 8 | QUADRA POLIESP. |
| 2 | LOJA | 9 | RESTAUR. / CAFETERIA |
| 3 | SERVIÇO | 10 | QUADRA VOLÊI |
| 4 | BAR | 11 | GOLF |
| 5 | RESTAURANTE- HÓSPEDES | 12 | SPA |
| 6 | APARTAMENTOS | 13 | YOGA / PILATES |
| 7 | BANGALÔS | 14 | PISCINA AQUECIDA |

ATELIÊ IV - RESORT SOLARA		PRANCHA: 01/01
ORIENTADO POR:	CLÓVIS AQUINO, LARISSA ANDARA, PRISCILA LOUREIRO	
PROJETADO POR:	EMANUELLY FERREIRA, KAROLAINÉ KOHLER E MARIANA GOTTARDO	